

DEVELOPMENT APPLICATION MODIFICATION

DRAWING REGISTER

SHEET NO.	SHEET NAME
DA.A100	TITLE SHEET
DA.A101	SUMMARY PAGE
DA.A102	SITE ANALYSIS PAGE
DA.A103	SITE PLAN
DA.A104	EXISTING BASE BUILDING
DA.A105	GROUND FLOOR PLAN
DA.A106	FIRST FLOOR PLAN
DA.A107	ROOF PLAN
DA.A108	SECONDARY DWELLING
DA.A109	BASIX SCHEDULE
DA.A110	BASIX SCHEDULE CONT.
DA.A200	EAST & NORTH ELEVATIONS
DA.A201	WEST & SOUTH ELEVATIONS
DA.A300	SOUTH, EAST & NORTH SECTIONS
DA.A301	WEST SECTIONS
DA.A500	WINDOW & DOOR SCHEDULE
DA.A501	WINDOW & DOOR SCHEDULE CONT.
DA.A502	SHADOW DIAGRAMS
DA.A503	SITE WASTE MANAGEMENT PLAN



Street View



Site Location Map

DEVELOPMENT APPLICATION MODIFICATION

DO NOT USE THIS DRAWING FOR CONSTRUCTION UNLESS DESIGNATED



BUILDING DESIGN
INTERIOR DESIGN
PROJECT MANAGEMENT
DEVELOPMENT APPROVALS



www.emvy.com.au
design@emvy.com.au
0492 924 763
+612 4283 2685

North

ISSUE No
DA
DA

DESCRIPTION
DEVELOPMENT APPLICATION
DA MODIFICATION

DRAWN BY
MV
MV

CHECKED BY
CA
CA

DATE
25/02/26
25/05/26

NOTE TO BUILDER
Figured dimensions shall be used.
Do not scale drawing.
The contractor shall verify all dimensions on site prior to commencement of work.
All work to comply with the National Code of Construction (NCC 2022) & Australia Standards.

CLIENT AGREEMENT
As the client I have read and approved all the drawings and specifications of the drawings.

approved

CLIENT
A & B CHRISTIE-DAVID
PROJECT NAME
ALTERATIONS & ADDITIONS
PROJECT ADDRESS
LOT 15 SEC M DP 2697
16 ALFRED STREET
WOONONA NSW 2517

PROJECT #
186.25

SCALE
As noted @ A3


SHEET NAME
CONTENTS PAGE
SHEET NO.

DA. A100


REVISION #

1

 Boundary Line
 Demolish

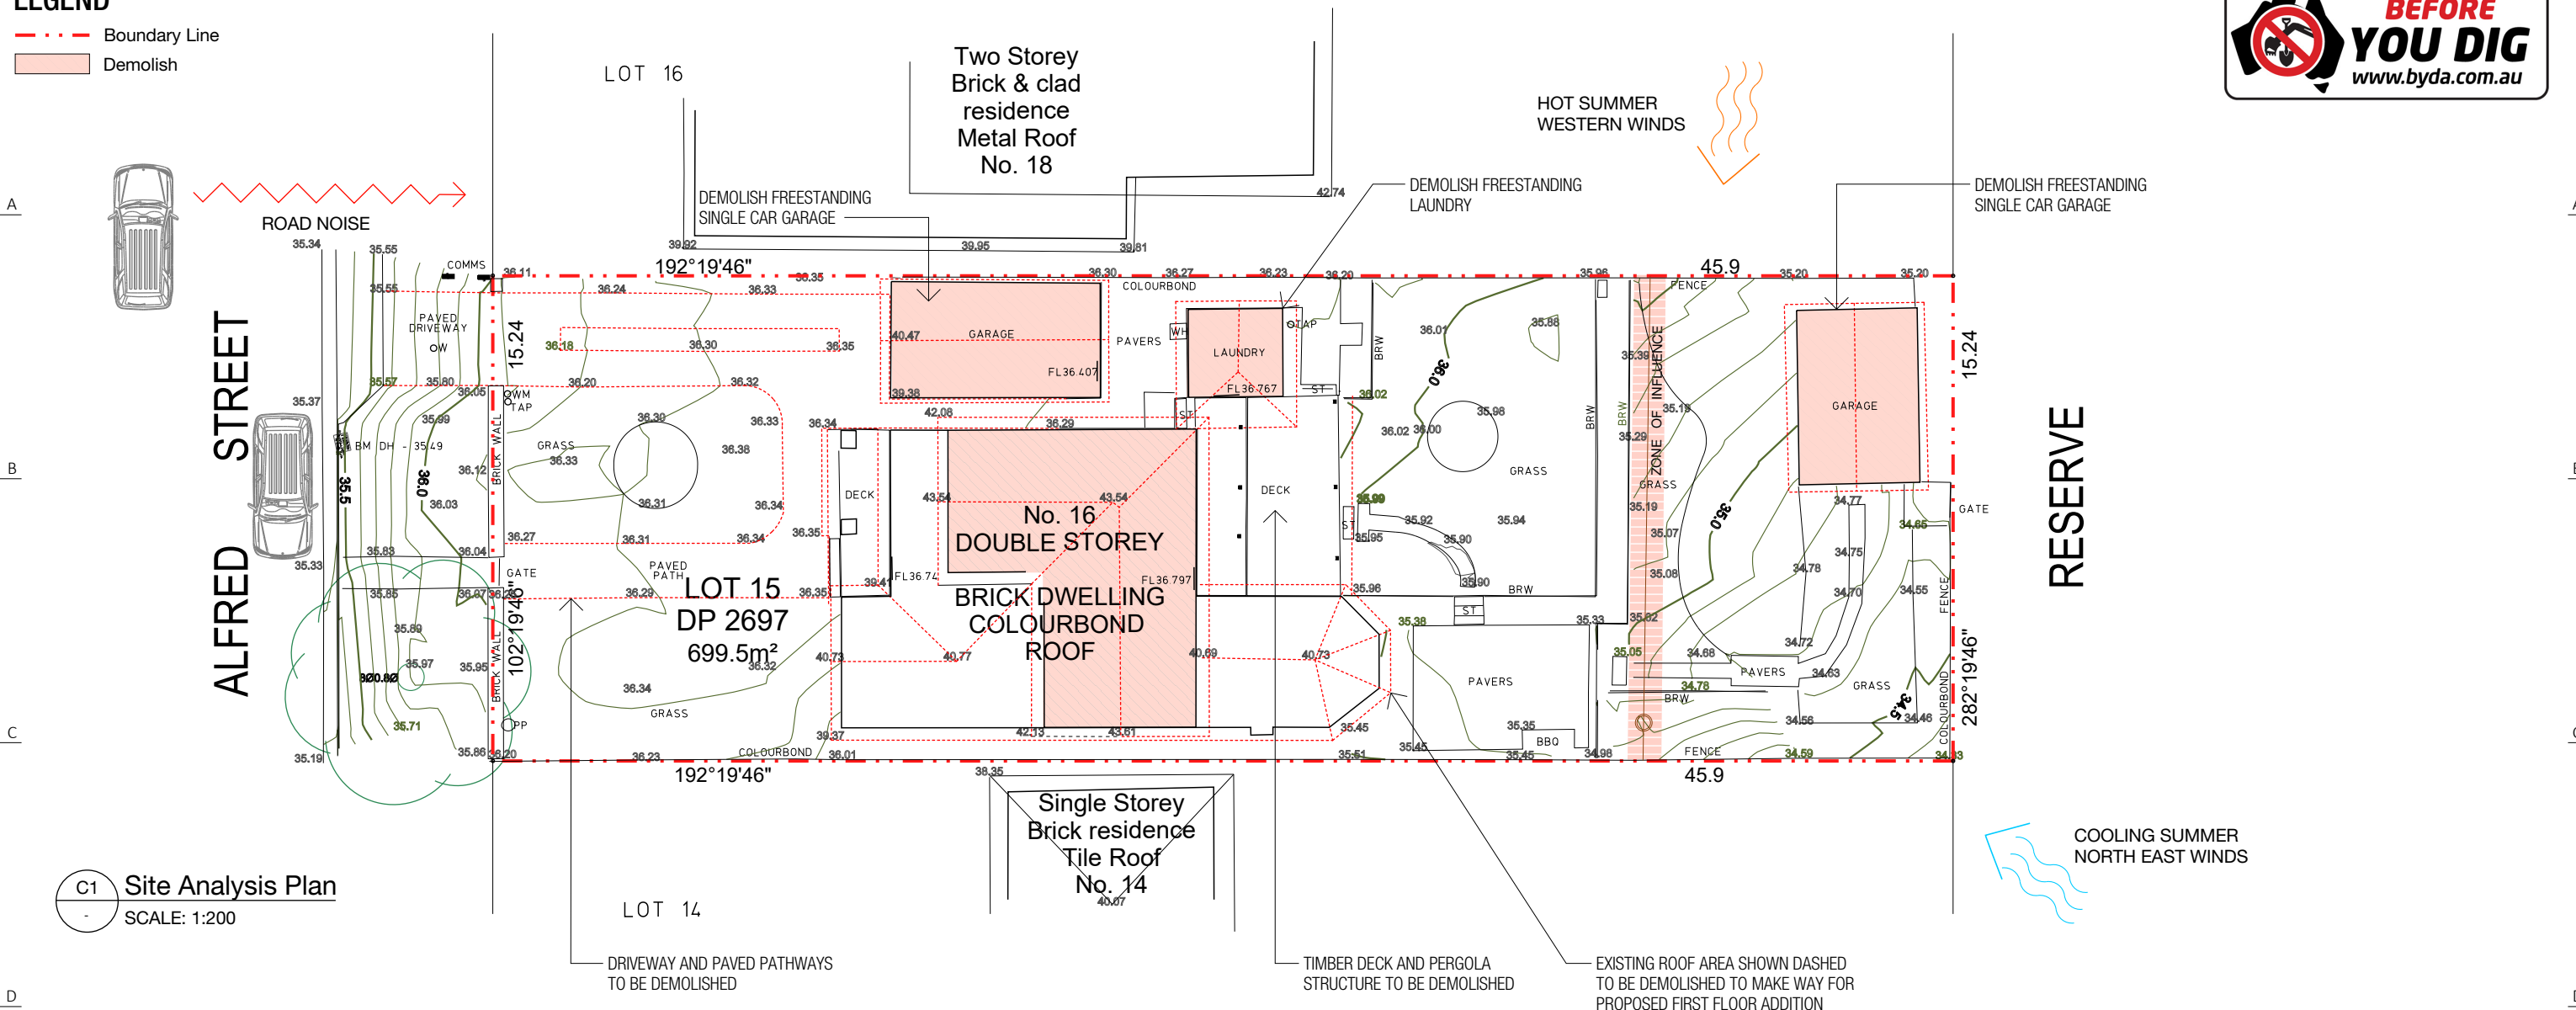

SOLAR PATH DIAGRAM

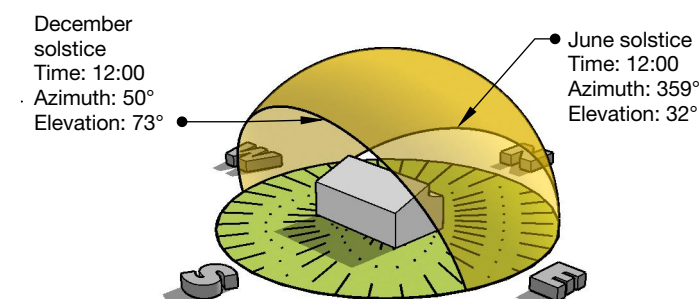


DEVELOPMENT APPLICATION MODIFICATION

DO NOT USE THIS DRAWING FOR CONSTRUCTION UNLESS DESIGNATED

 BUILDING DESIGN INTERIOR DESIGN PROJECT MANAGEMENT DEVELOPMENT APPROVALS	 www.emvy.com.au design@emvy.com.au 0492 924 763 +612 4283 2685	North 	ISSUE No DA DA	DESCRIPTION DEVELOPMENT APPLICATION DA MODIFICATION	DRAWN BY MV MV	CHECKED BY CA CA	DATE 25/02/26 25/05/26	NOTE TO BUILDER Figured dimensions shall be used. Do not scale drawing. The contractor shall verify all dimensions on site prior to commencement of work. All work to comply with the National Code of Construction (NCC 2022) & Australia Standards.	CLIENT AGREEMENT As the client I have read and approved all the drawings and specifications of the drawings.	CLIENT A & B CHRISTIE-DAVID PROJECT NAME ALTERATIONS & ADDITIONS PROJECT ADDRESS LOT 15 SEC M DP 2697 16 ALFRED STREET WOONONA NSW 2517	PROJECT # 186.25 SCALE As noted @ A3
											SHEET NAME SITE ANALYSIS SHEET NO. DA. A102 REVISION # -

LEGEND

- Boundary Line
- Roof Line
- First Floor
- Ground Floor

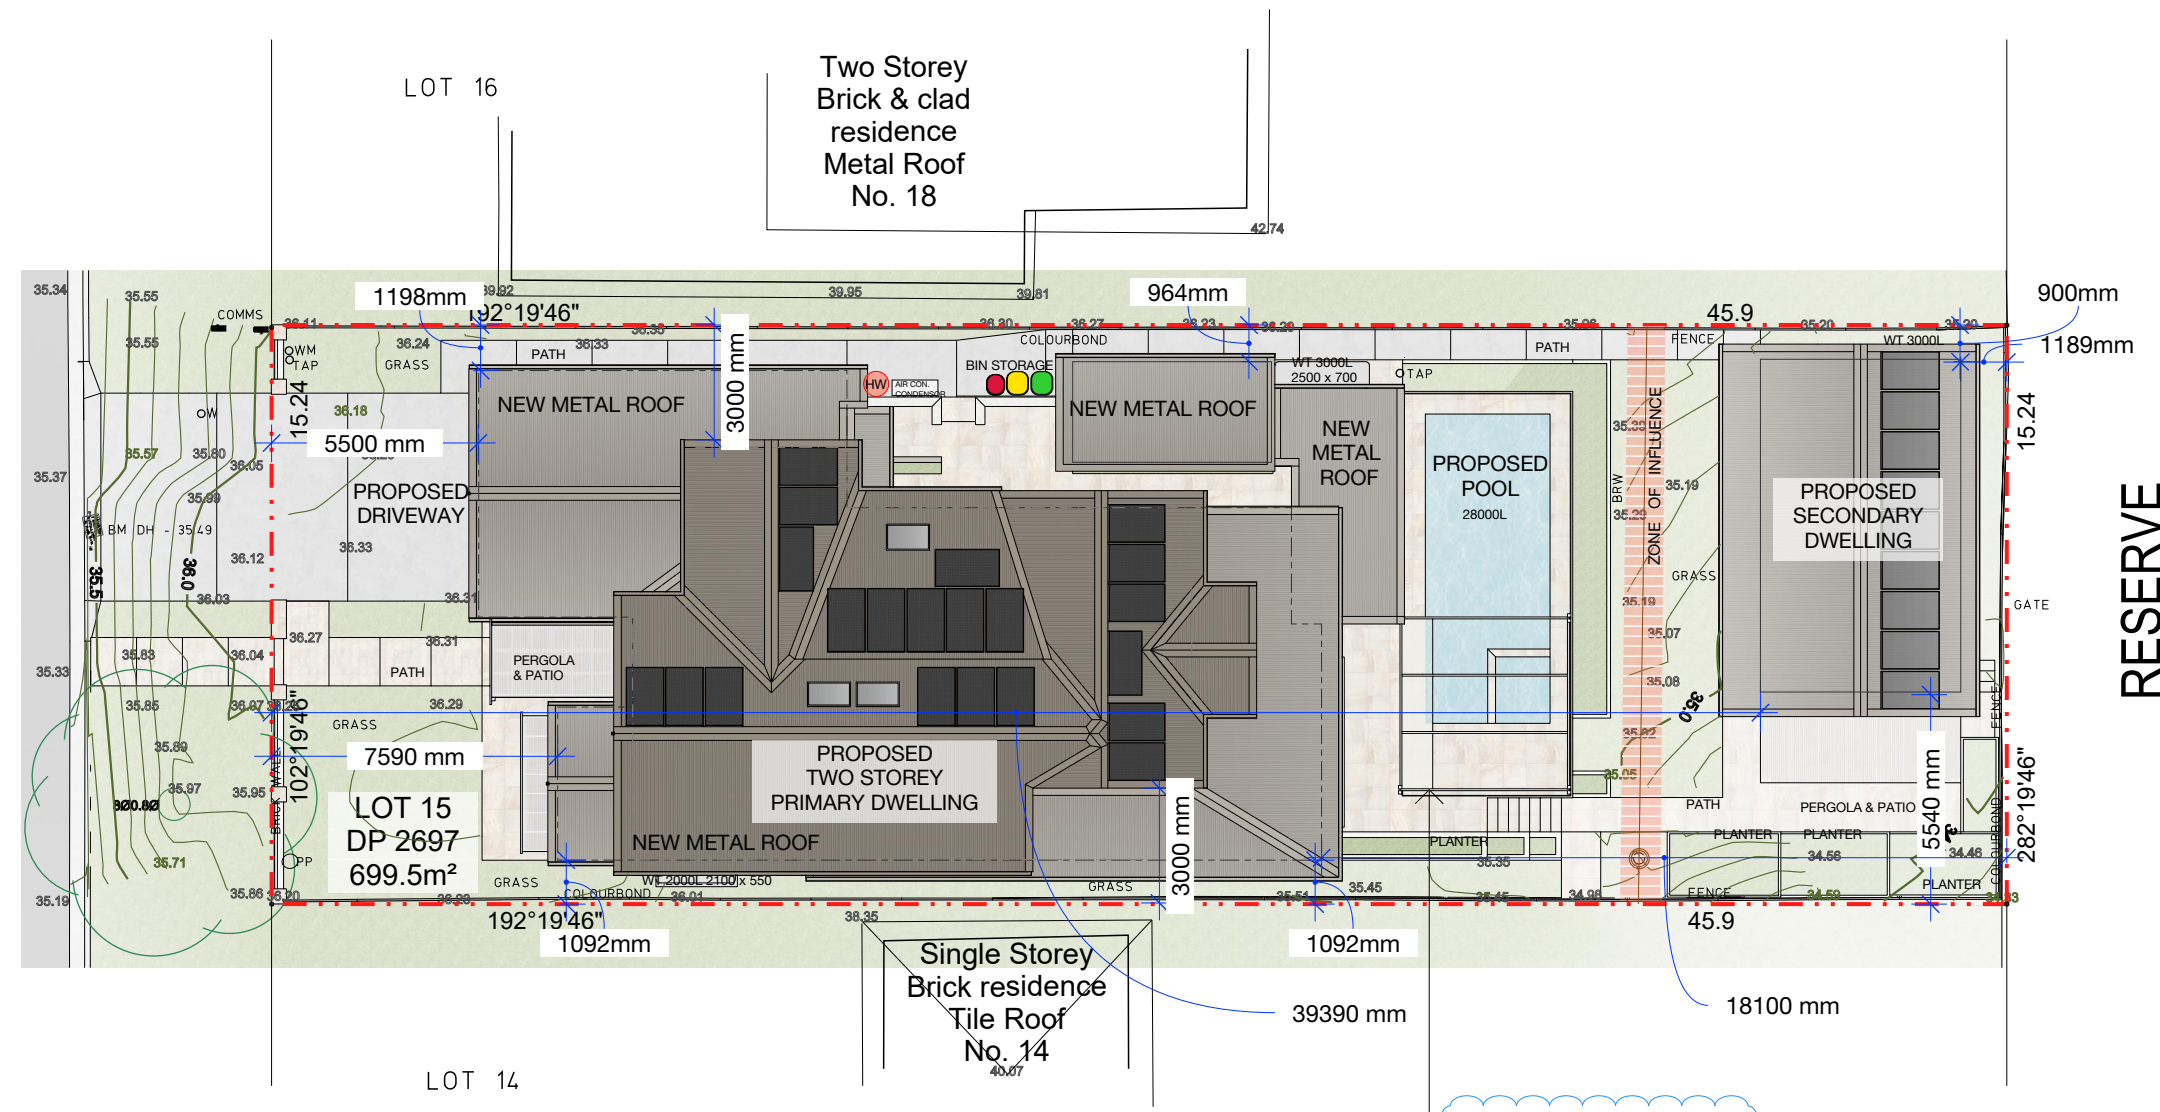

C1 Site Plan
SCALE: 1:200

ROOF AREA CALCULATIONS	
	EXISTING
PRIMARY DWELLING - CATCHABLE ROOF AREA	255m2
	PROPOSED
PRIMARY DWELLING - CATCHABLE ROOF AREA	306m2
SECONDARY DWELLING - CATCHABLE ROOF AREA	74m2

DEVELOPMENT APPLICATION MODIFICATION

DO NOT USE THIS DRAWING FOR CONSTRUCTION UNLESS DESIGNATED




BUILDING DESIGN
INTERIOR DESIGN
PROJECT MANAGEMENT
DEVELOPMENT APPROVALS



ACCREDITED
BUILDING DESIGNER

www.emvy.com.au
design@emvy.com.au
0492 924 763
+612 4283 2685

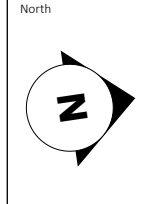

ISSUE No DA DA	DESCRIPTION DEVELOPMENT APPLICATION DA MODIFICATION	DRAWN BY MV MV	CHECKED BY CA CA	DATE 25/02/26 25/05/26
----------------------	---	----------------------	------------------------	------------------------------



NOTE TO BUILDER
Figured dimensions shall be used.
Do not scale drawing.
The contractor shall verify all dimensions on site prior to commencement of work.
All work to comply with the National Code of Construction (NCC 2022) & Australia Standards.

CLIENT AGREEMENT
As the client I have read and approved all the drawings and specifications of the drawings.

CLIENT
A & B CHRISTIE-DAVID
PROJECT NAME
ALTERATIONS & ADDITIONS
PROJECT ADDRESS
LOT 15 SEC M DP 2697
16 ALFRED STREET
WOONONA NSW 2517

PROJECT # 186.25	SCALE As noted @ A3
SHEET NAME SITE PLAN	REVISION #
SHEET NO. DA.A103	1

- LEGEND**
- Boundary Line
 - Roof Line
 - Ground Floor
 - Demolition

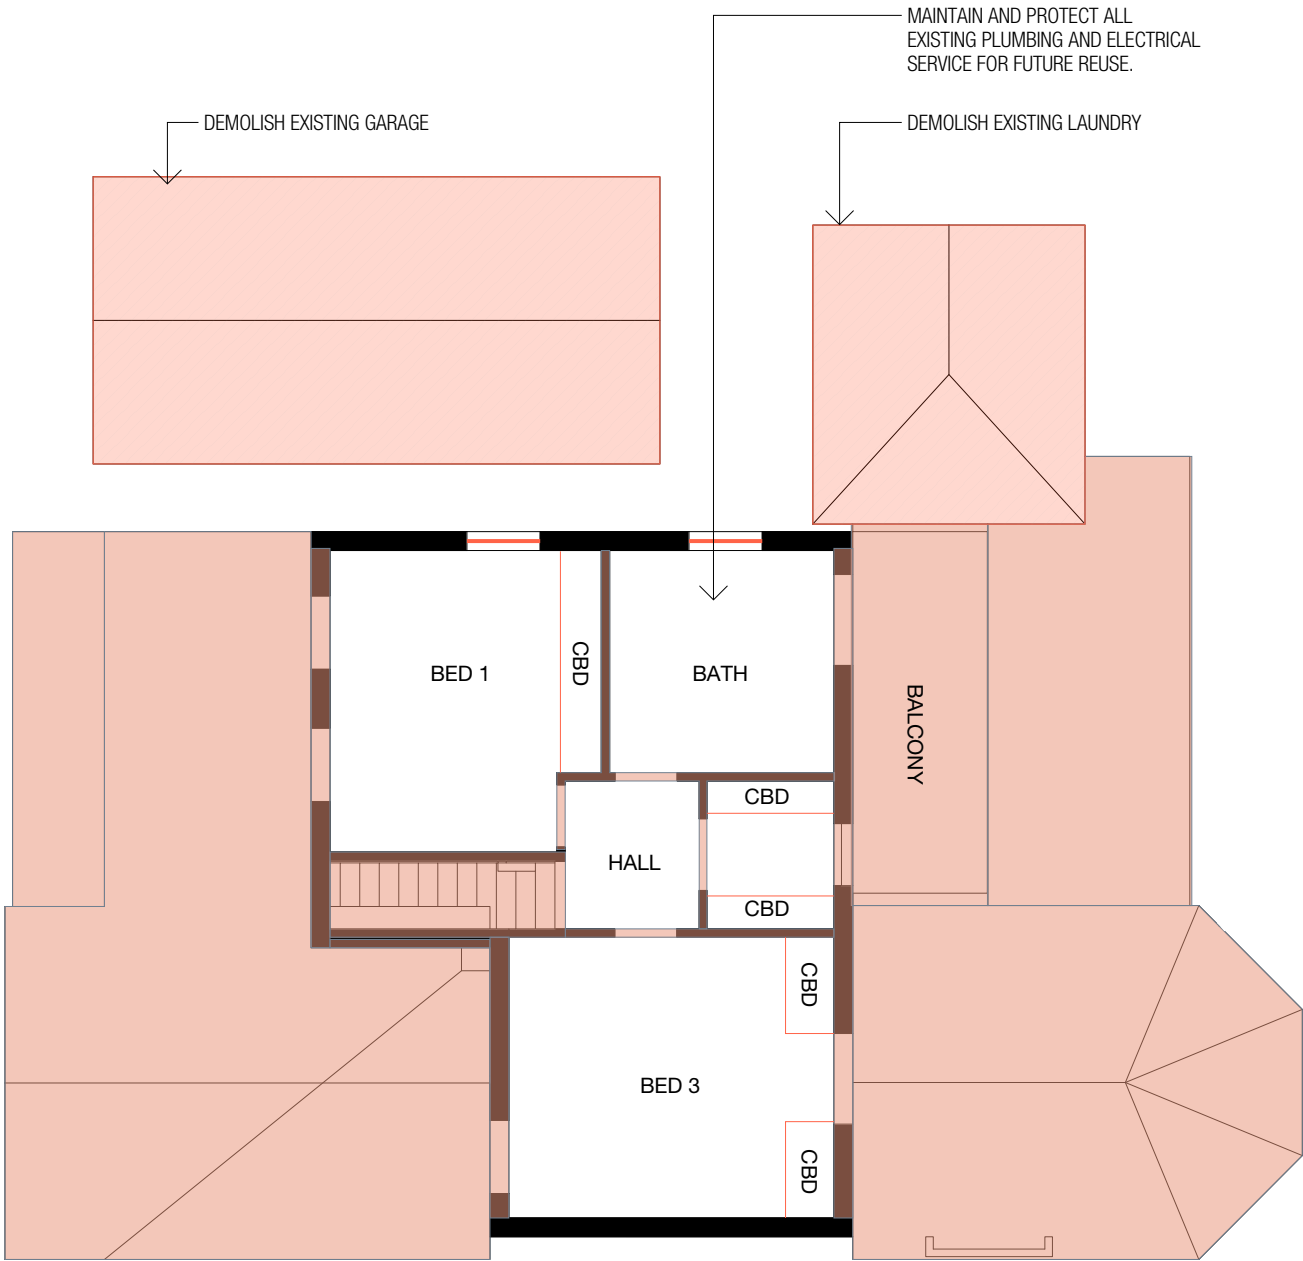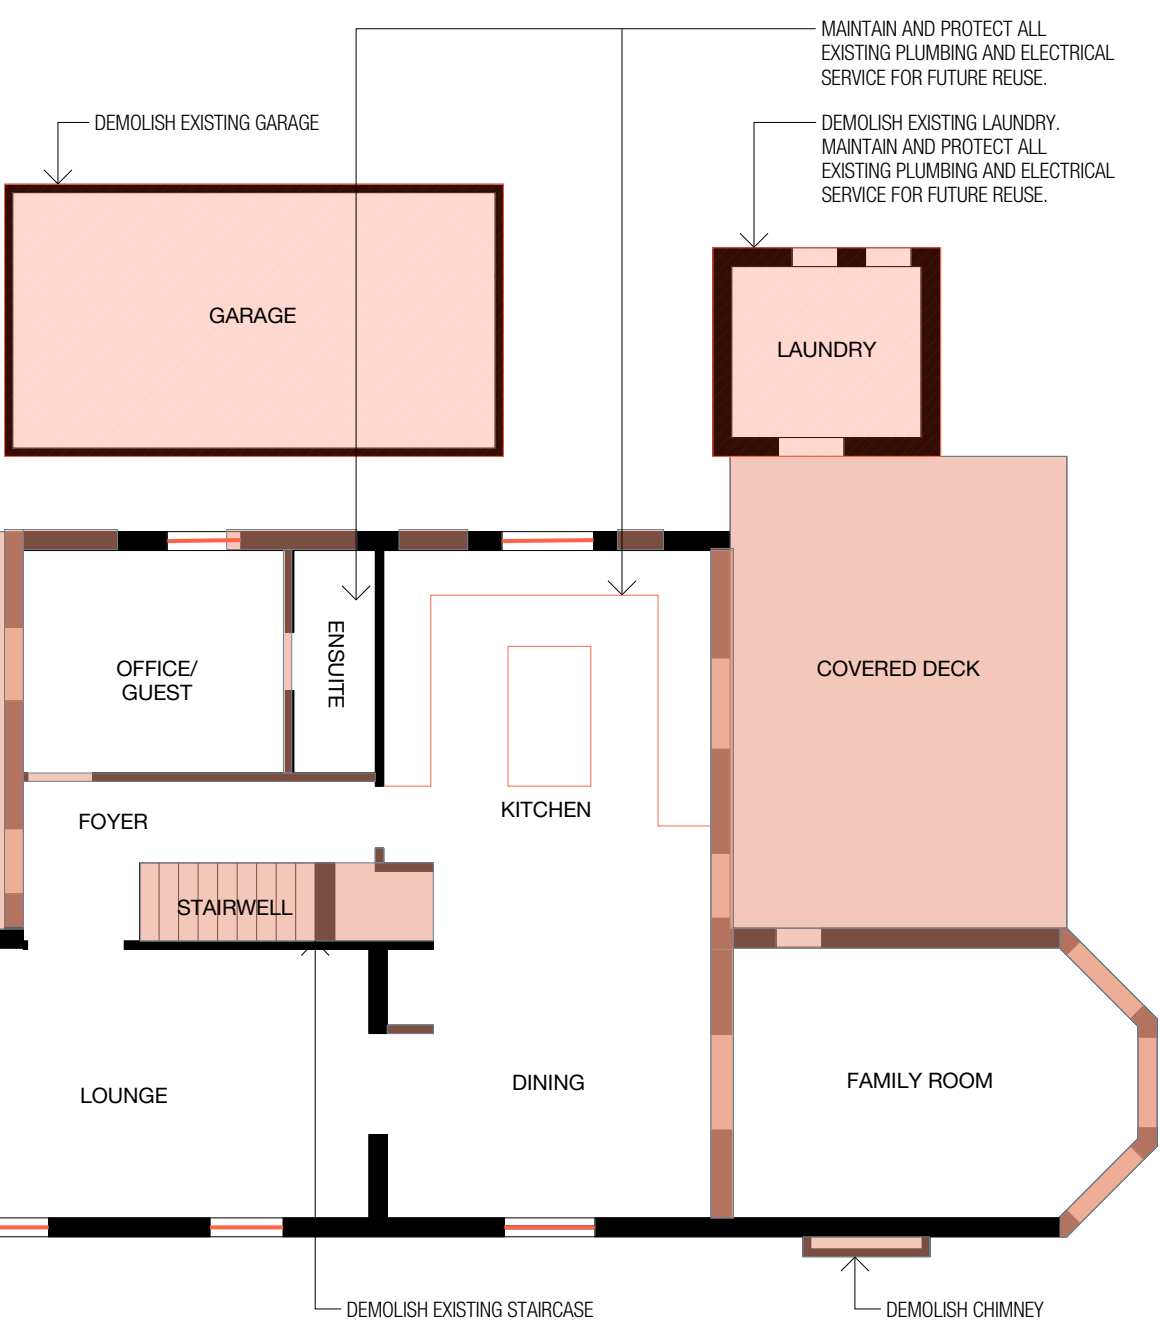

F1 Existing Ground Floor Plan
SCALE: 1:100

F5 Existing First Floor Plan
SCALE: 1:100


DEVELOPMENT APPLICATION MODIFICATION
DO NOT USE THIS DRAWING FOR CONSTRUCTION UNLESS DESIGNATED



BUILDING DESIGN
INTERIOR DESIGN
PROJECT MANAGEMENT
DEVELOPMENT APPROVALS



www.emvy.com.au
design@emvy.com.au
0492 924 763
+612 4283 2685

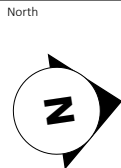

ISSUE No
DA
DA

DESCRIPTION
DEVELOPMENT APPLICATION
DA MODIFICATION

DRAWN BY
MV
MV

CHECKED BY
CA
CA

DATE
25/02/26
25/05/26

NOTE TO BUILDER
Figured dimensions shall be used.
Do not scale drawing.
The contractor shall verify all dimensions on site prior to commencement of work.
All work to comply with the National Code of Construction (NCC 2022) & Australia Standards.

CLIENT AGREEMENT
As the client I have read and approved all the drawings and specifications of the drawings.

approved

CLIENT
A & B CHRISTIE-DAVID
PROJECT NAME
ALTERATIONS & ADDITIONS
PROJECT ADDRESS
LOT 15 SEC M DP 2697
16 ALFRED STREET
WOONONA NSW 2517

PROJECT #
186.25

SCALE
As noted @ A3

SHEET NAME
EX BASE BUILDING
SHEET NO.

DA.A104

REVISION #

-

LEGEND


- Boundary Line
- Roof Line
- First Floor
- Ground Floor
- Ex. Building Line
- Pool Fence

SWIMMING POOL REQUIRMENTS

THE DESIGN AND CONSTRUCTION OF THE SWIMMING POOL AND ASSOCIATED FENCING AND EQUIPMENT MUST COMPLY WITH:

- THE SWIMMING POOLS ACT 1992 & REGULATION 2018
- BUILDING CODE OF AUSTRALIA
- AUSTRALIAN STANDARD 1926.1-2012 - SWIMMING POOL SAFETY
- COUNCILS DEVELOPMENT CONTROL. AND
- PROTECTION OF THE ENVIRONMENT OPERATIONS ACT 1997.

NO WATER MUST BE PLACED IN THE POOL/SPA UNTIL THE SAFETY FENCES HAVE BEEN COMPLETED IN ACCORDANCE WITH THE APPROVED PLANS AND SPECIFICATIONS AND INSPECTED BY THE PRINCIPAL CERTIFIER.

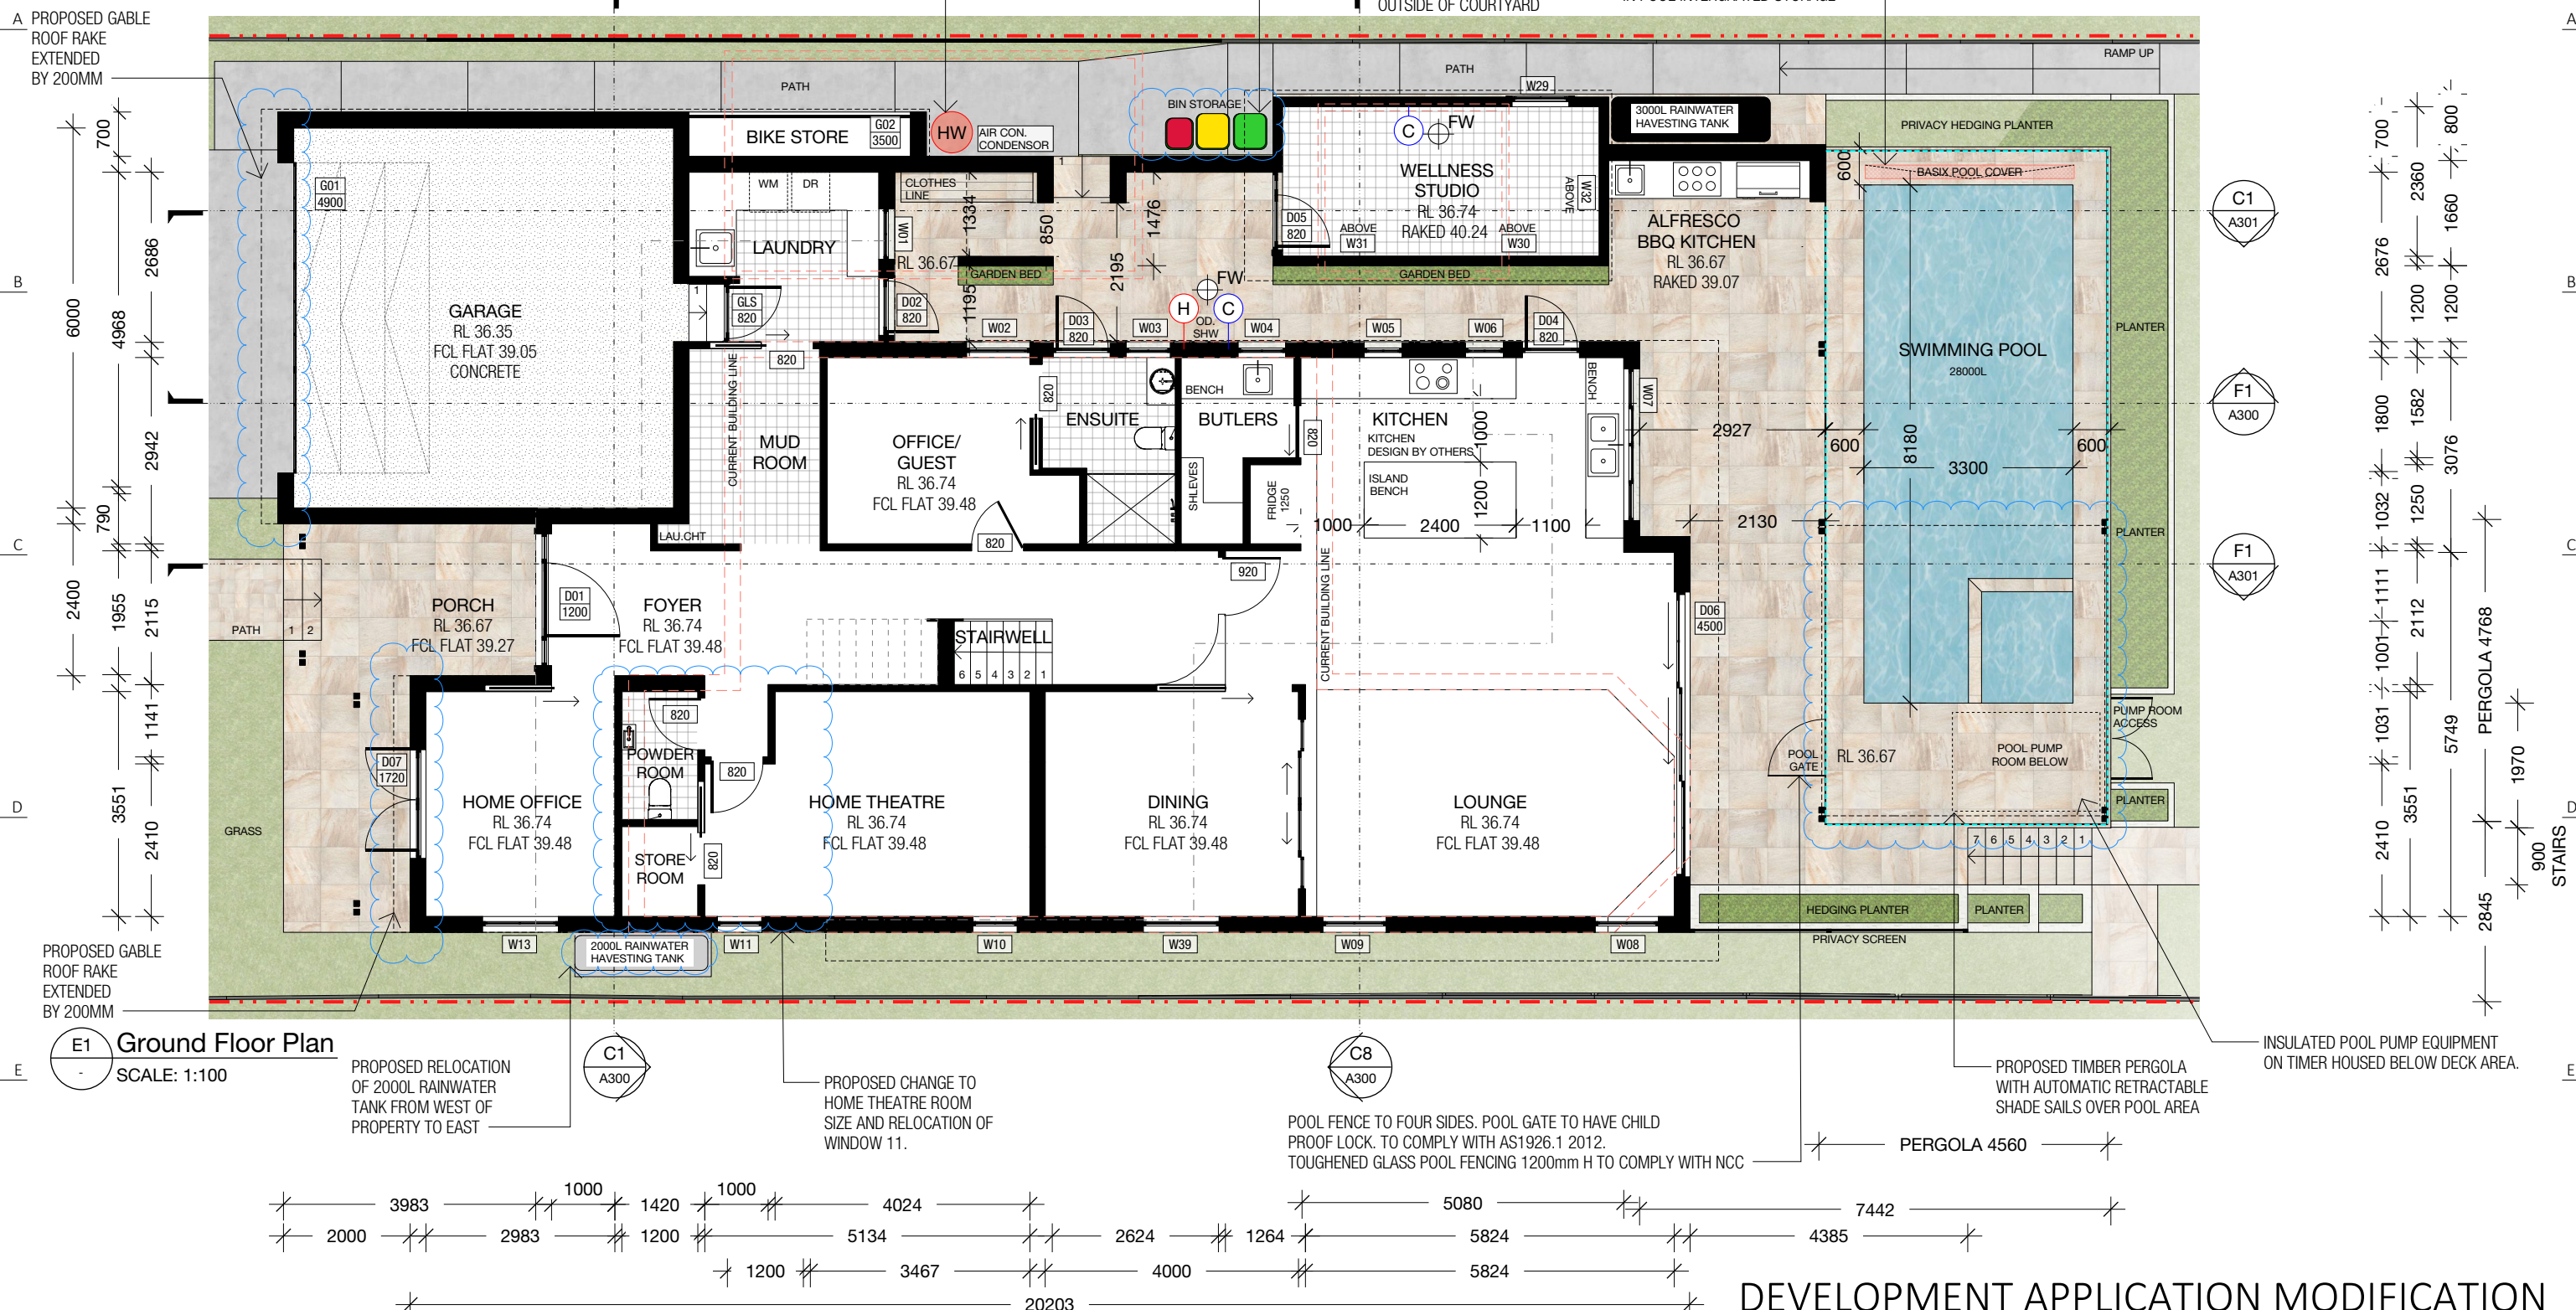



DEVELOPMENT APPLICATION MODIFICATION

DO NOT USE THIS DRAWING FOR CONSTRUCTION UNLESS DESIGNATED

	BD&A ACCREDITED BUILDING DESIGNER www.emvy.com.au design@emvy.com.au 0492 924 763 +612 4283 2685	North	ISSUE No DA DA DESCRIPTION DEVELOPMENT APPLICATION DA MODIFICATION	DRAWN BY MV MV CHECKED BY CA CA	DATE 25/02/26 25/05/26 NOTE TO BUILDER Figured dimensions shall be used. Do not scale drawing. The contractor shall verify all dimensions on site prior to commencement of work. All work to comply with the National Code of Construction (NCC 2022) & Australia Standards.	CLIENT AGREEMENT As the client I have read and approved all the drawings and specifications of the drawings. approved	CLIENT A & B CHRISTIE-DAVID PROJECT NAME ALTERATIONS & ADDITIONS PROJECT ADDRESS LOT 15 SEC M DP 2697 16 ALFRED STREET WOONONA NSW 2517	PROJECT # 186.25 SCALE As noted @ A3 SHEET NAME GROUND FLOOR PLAN SHEET NO. DA.A105 REVISION # 1
--	---	--------------	--	---	--	---	--	---

LEGEND

- Boundary Line
- Roof Line
- First Floor
- Ground Floor
- Ex. Building Line

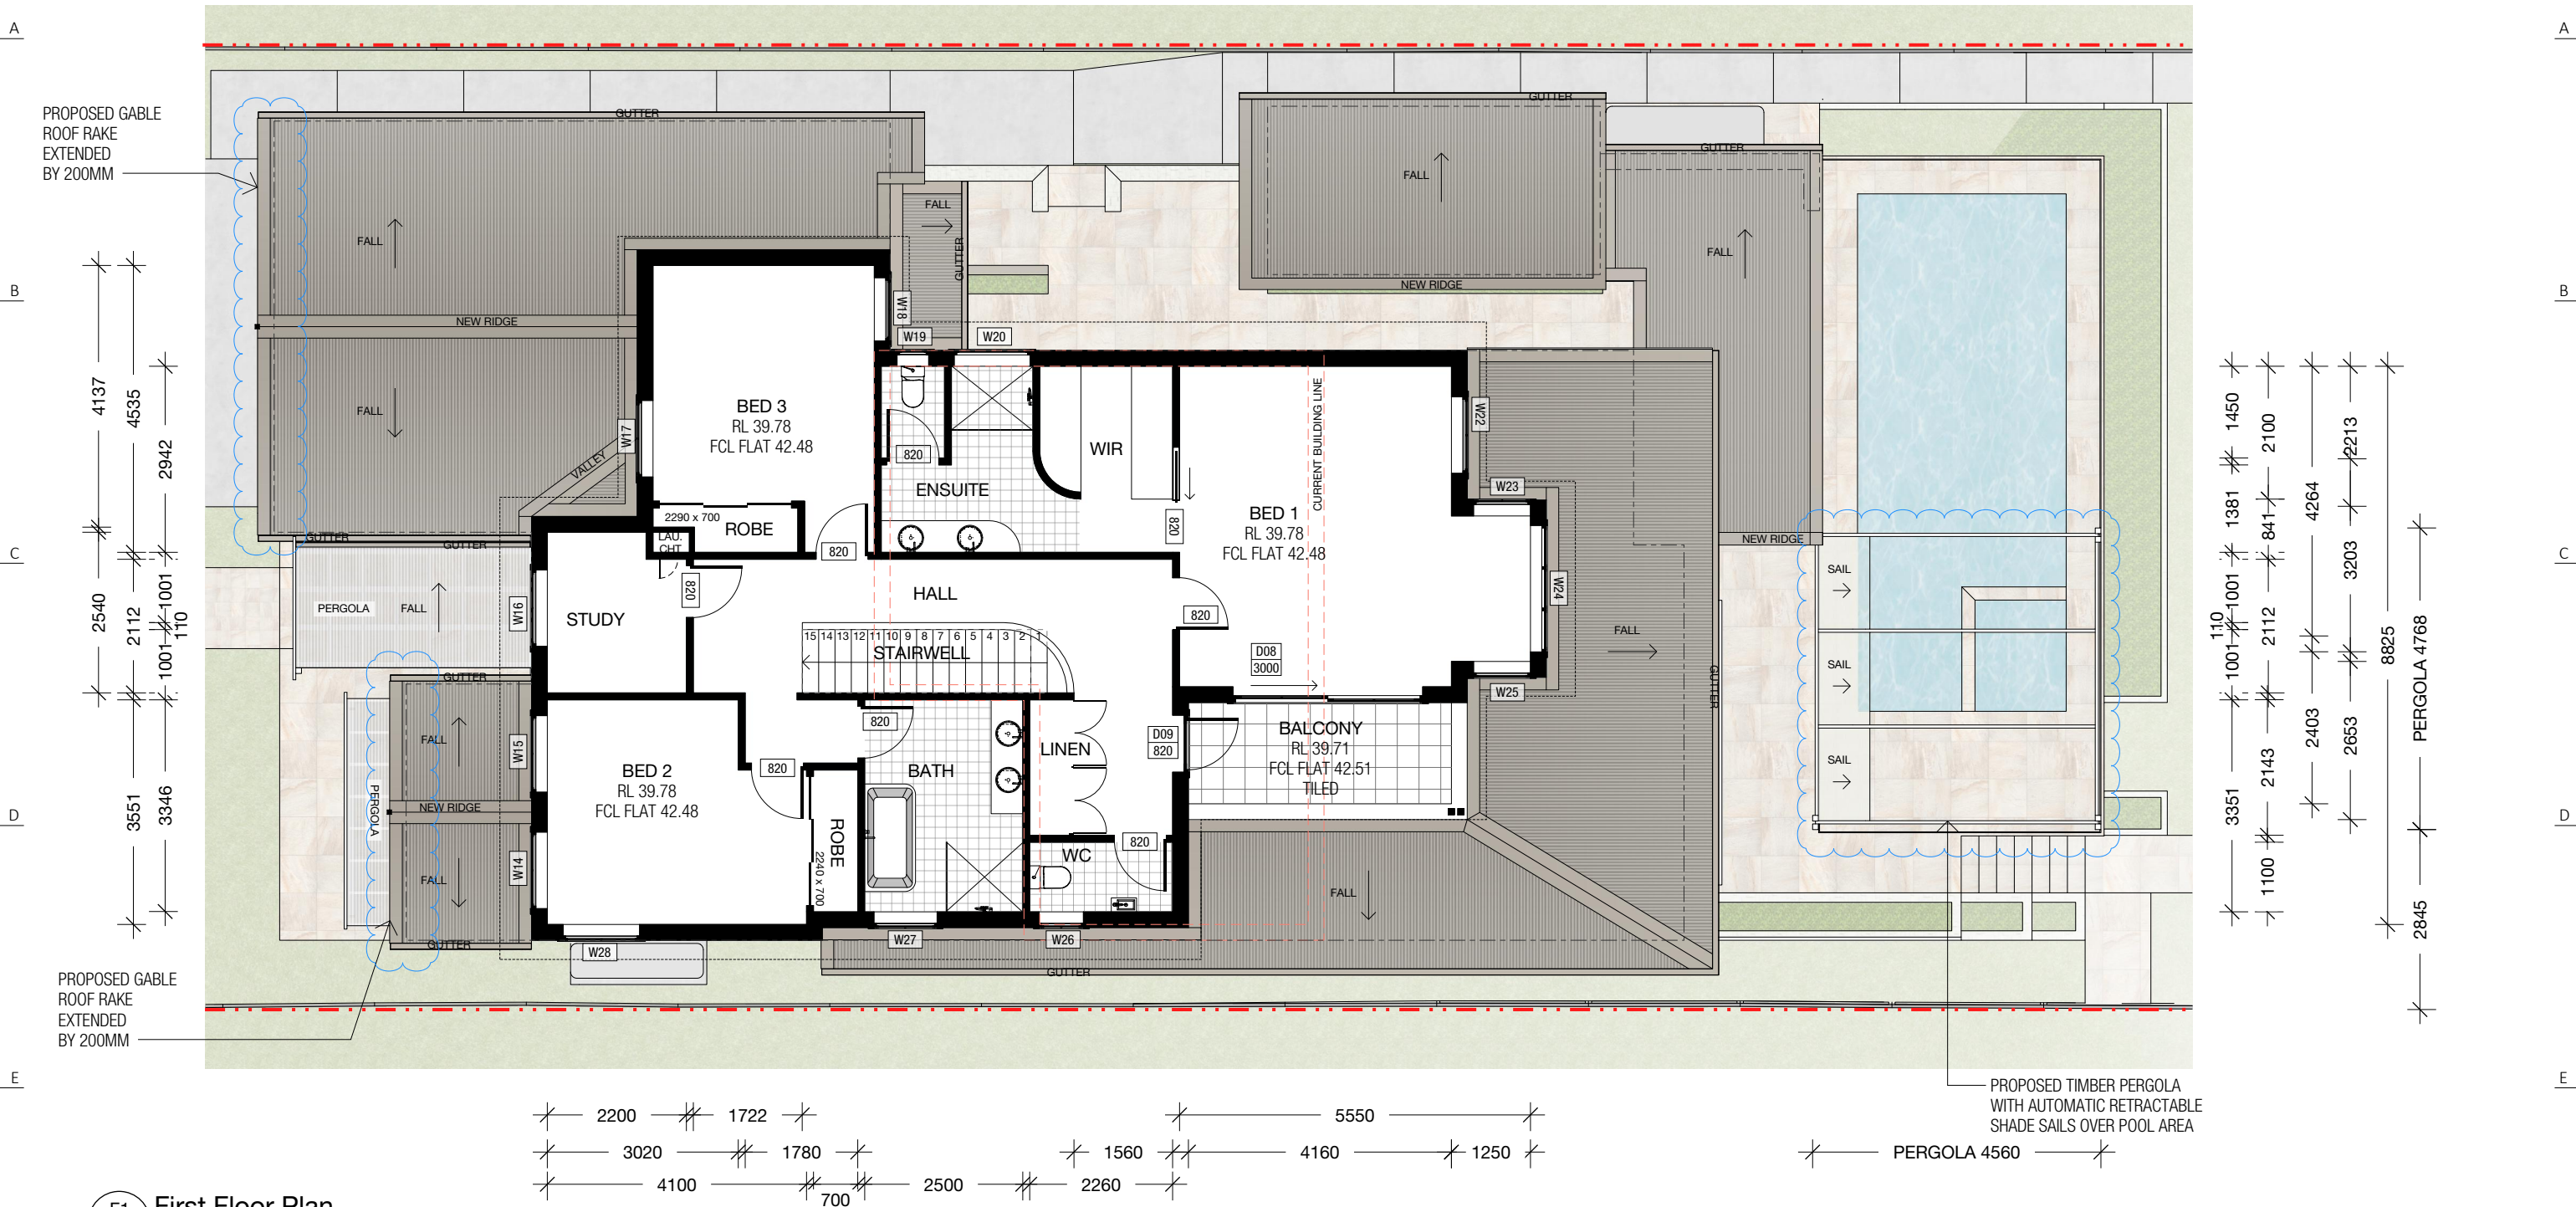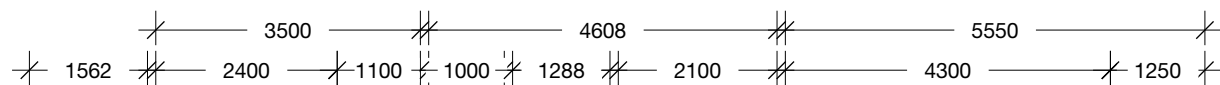

F1 First Floor Plan
SCALE: 1:100

DEVELOPMENT APPLICATION MODIFICATION

DO NOT USE THIS DRAWING FOR CONSTRUCTION UNLESS DESIGNATED


 BUILDING DESIGN INTERIOR DESIGN PROJECT MANAGEMENT DEVELOPMENT APPROVALS	 www.emvy.com.au design@emvy.com.au 0492 924 763 +612 4283 2685	North 	ISSUE No DA DA DESCRIPTION DEVELOPMENT APPLICATION DA MODIFICATION	DRAWN BY MV MV CHECKED BY CA CA	DATE 25/02/26 25/05/26	NOTE TO BUILDER Figured dimensions shall be used. Do not scale drawing. The contractor shall verify all dimensions on site prior to commencement of work. All work to comply with the National Code of Construction (NCC 2022) & Australia Standards.	CLIENT AGREEMENT As the client I have read and approved all the drawings and specifications of the drawings. approved	CLIENT A & B CHRISTIE-DAVID PROJECT NAME ALTERATIONS & ADDITIONS PROJECT ADDRESS LOT 15 SEC M DP 2697 16 ALFRED STREET WOONONA NSW 2517	PROJECT # 186.25 SCALE As noted @ A3 SHEET NAME FIRST FLOOR PLAN SHEET NO. DA.A106 REVISION # 1
--	---	---	---	--	------------------------------	---	---	--	--

LEGEND

- Boundary Line
- Roof Line
- First Floor
- Ground Floor
- Ex. Building Line

ROOF AREA CALCULATIONS	
	EXISTING
PRIMARY DWELLING - CATCHABLE ROOF AREA	255m2
	PROPOSED
PRIMARY DWELLING - CATCHABLE ROOF AREA	306m2
SECONDARY DWELLING - CATCHABLE ROOF AREA	74m2

BASIX NOTE: INSTALLATION OF PHOTOVOLTAIC SYSTEM WITH A CAPACITY TO GENERATE AT LEAST 2.6 PEAK KILOWATTS OF ELECTRICITY. SYSTEM TO BE CONNECTED TO DEVELOPMENT ELECTRICAL SYSTEM

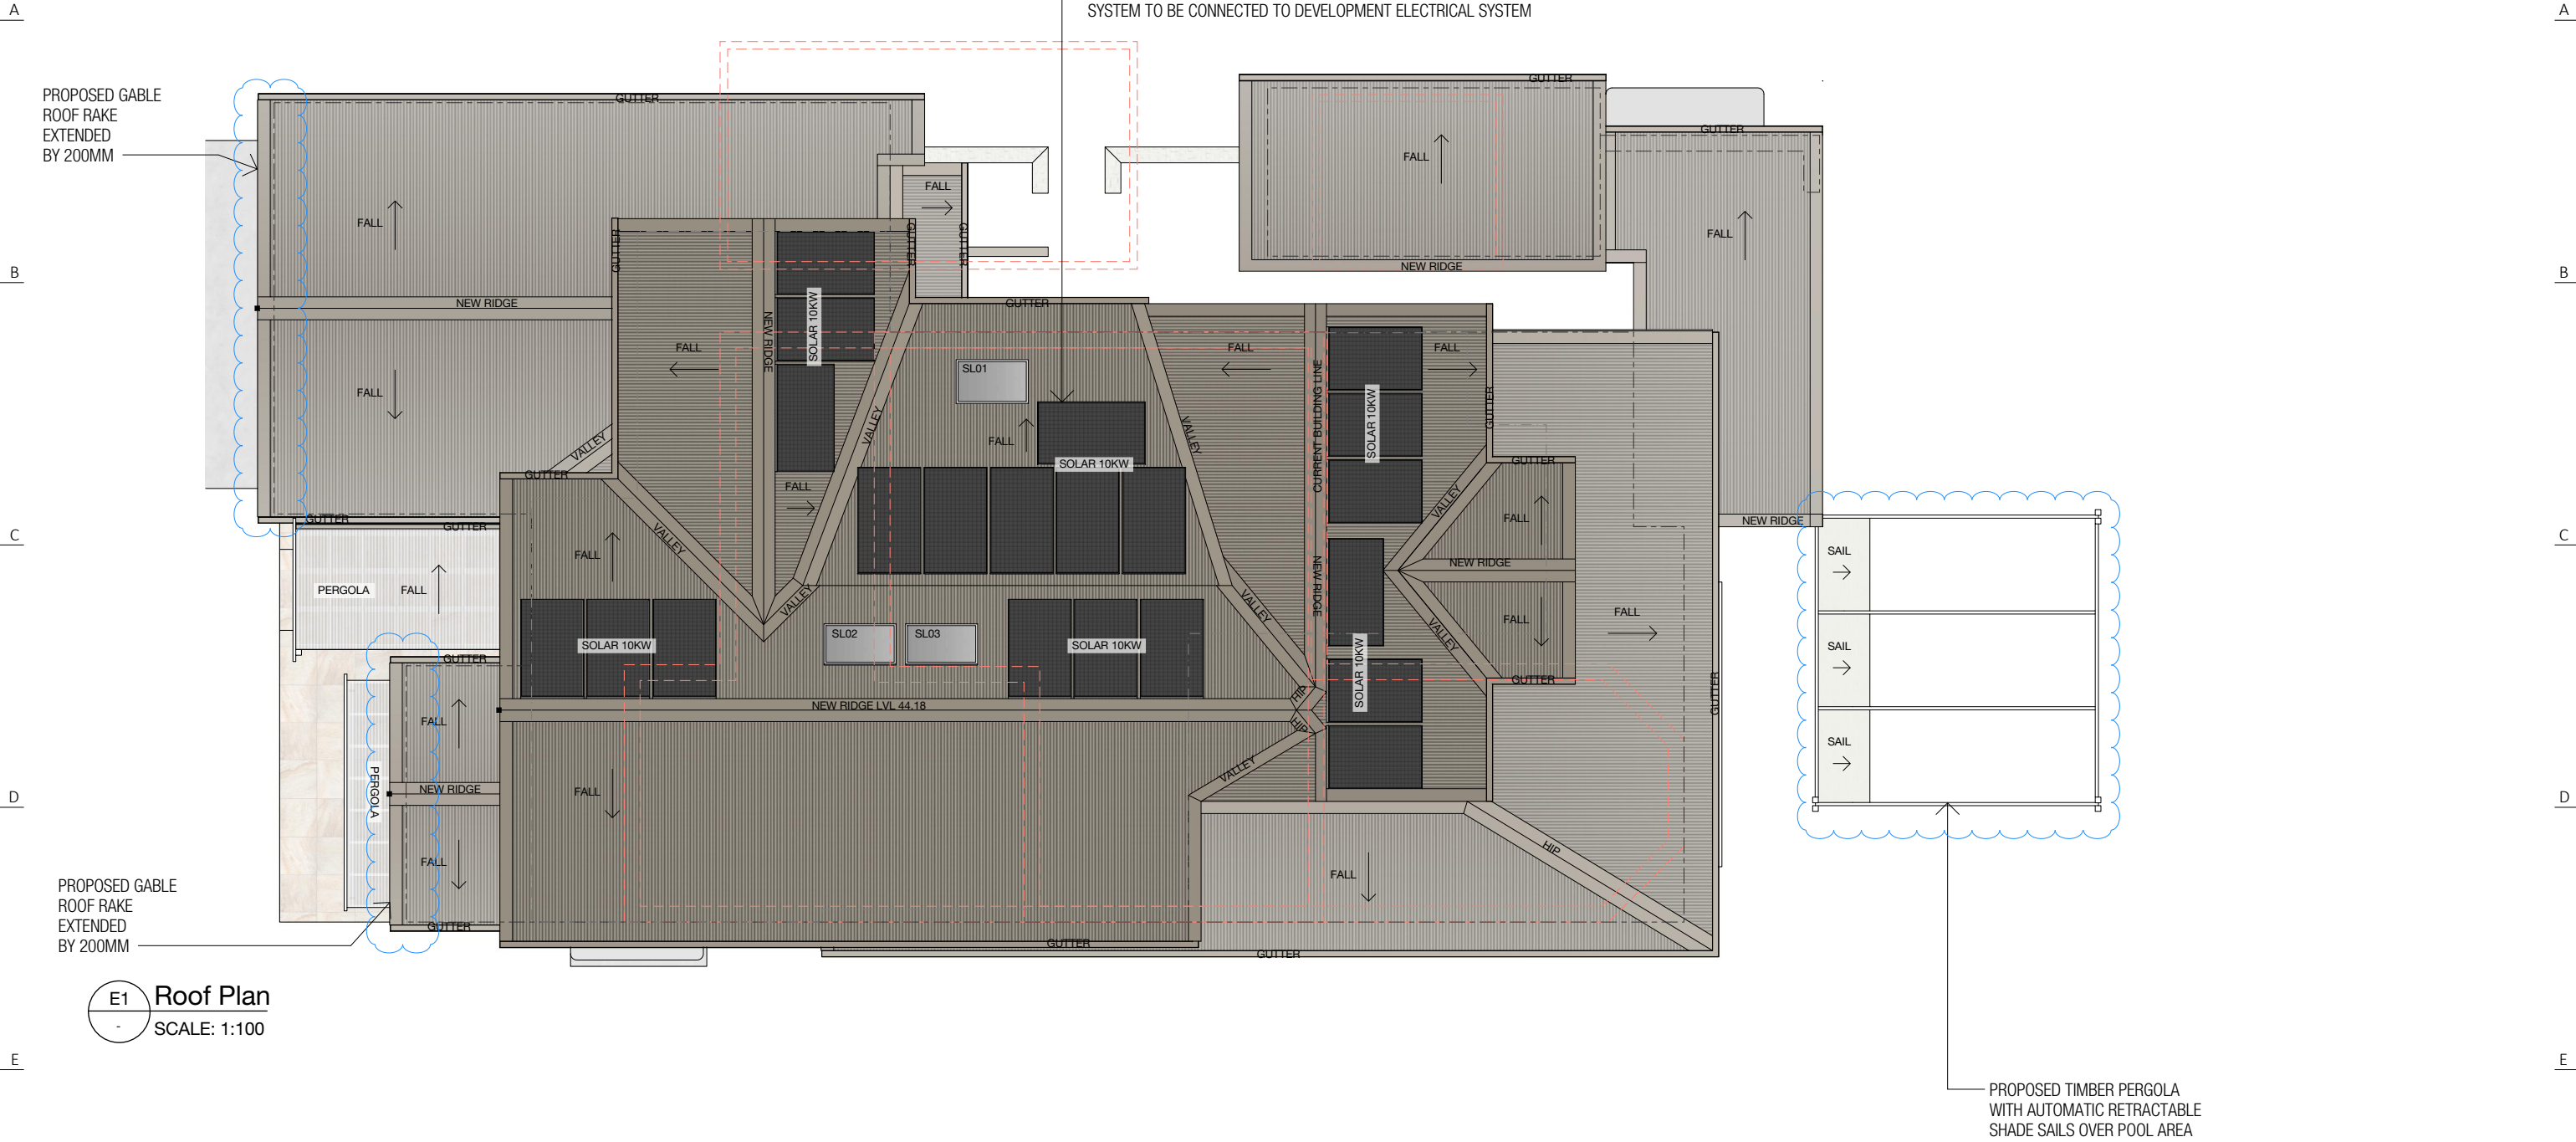

E1 Roof Plan
SCALE: 1:100


DEVELOPMENT APPLICATION MODIFICATION
DO NOT USE THIS DRAWING FOR CONSTRUCTION UNLESS DESIGNATED



BUILDING DESIGN
INTERIOR DESIGN
PROJECT MANAGEMENT
DEVELOPMENT APPROVALS



www.emvy.com.au
design@emvy.com.au
0492 924 763
+612 4283 2685

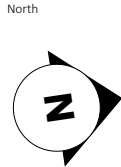

ISSUE No
DA
DA

DESCRIPTION
DEVELOPMENT APPLICATION
DA MODIFICATION

DRAWN BY
MV
MV

CHECKED BY
CA
CA

DATE
25/02/26
25/05/26

NOTE TO BUILDER
Figured dimensions shall be used.
Do not scale drawing.
The contractor shall verify all dimensions on site prior to commencement of work.
All work to comply with the National Code of Construction (NCC 2022) & Australia Standards.

CLIENT AGREEMENT
As the client I have read and approved all the drawings and specifications of the drawings.

approved

CLIENT
A & B CHRISTIE-DAVID
PROJECT NAME
ALTERATIONS & ADDITIONS
PROJECT ADDRESS
LOT 15 SEC M DP 2697
16 ALFRED STREET
WOONONA NSW 2517


PROJECT #
186.25

SCALE
As noted @ A3

SHEET NAME
ROOF PLAN
SHEET NO.

DA.A107

REVISION #
1

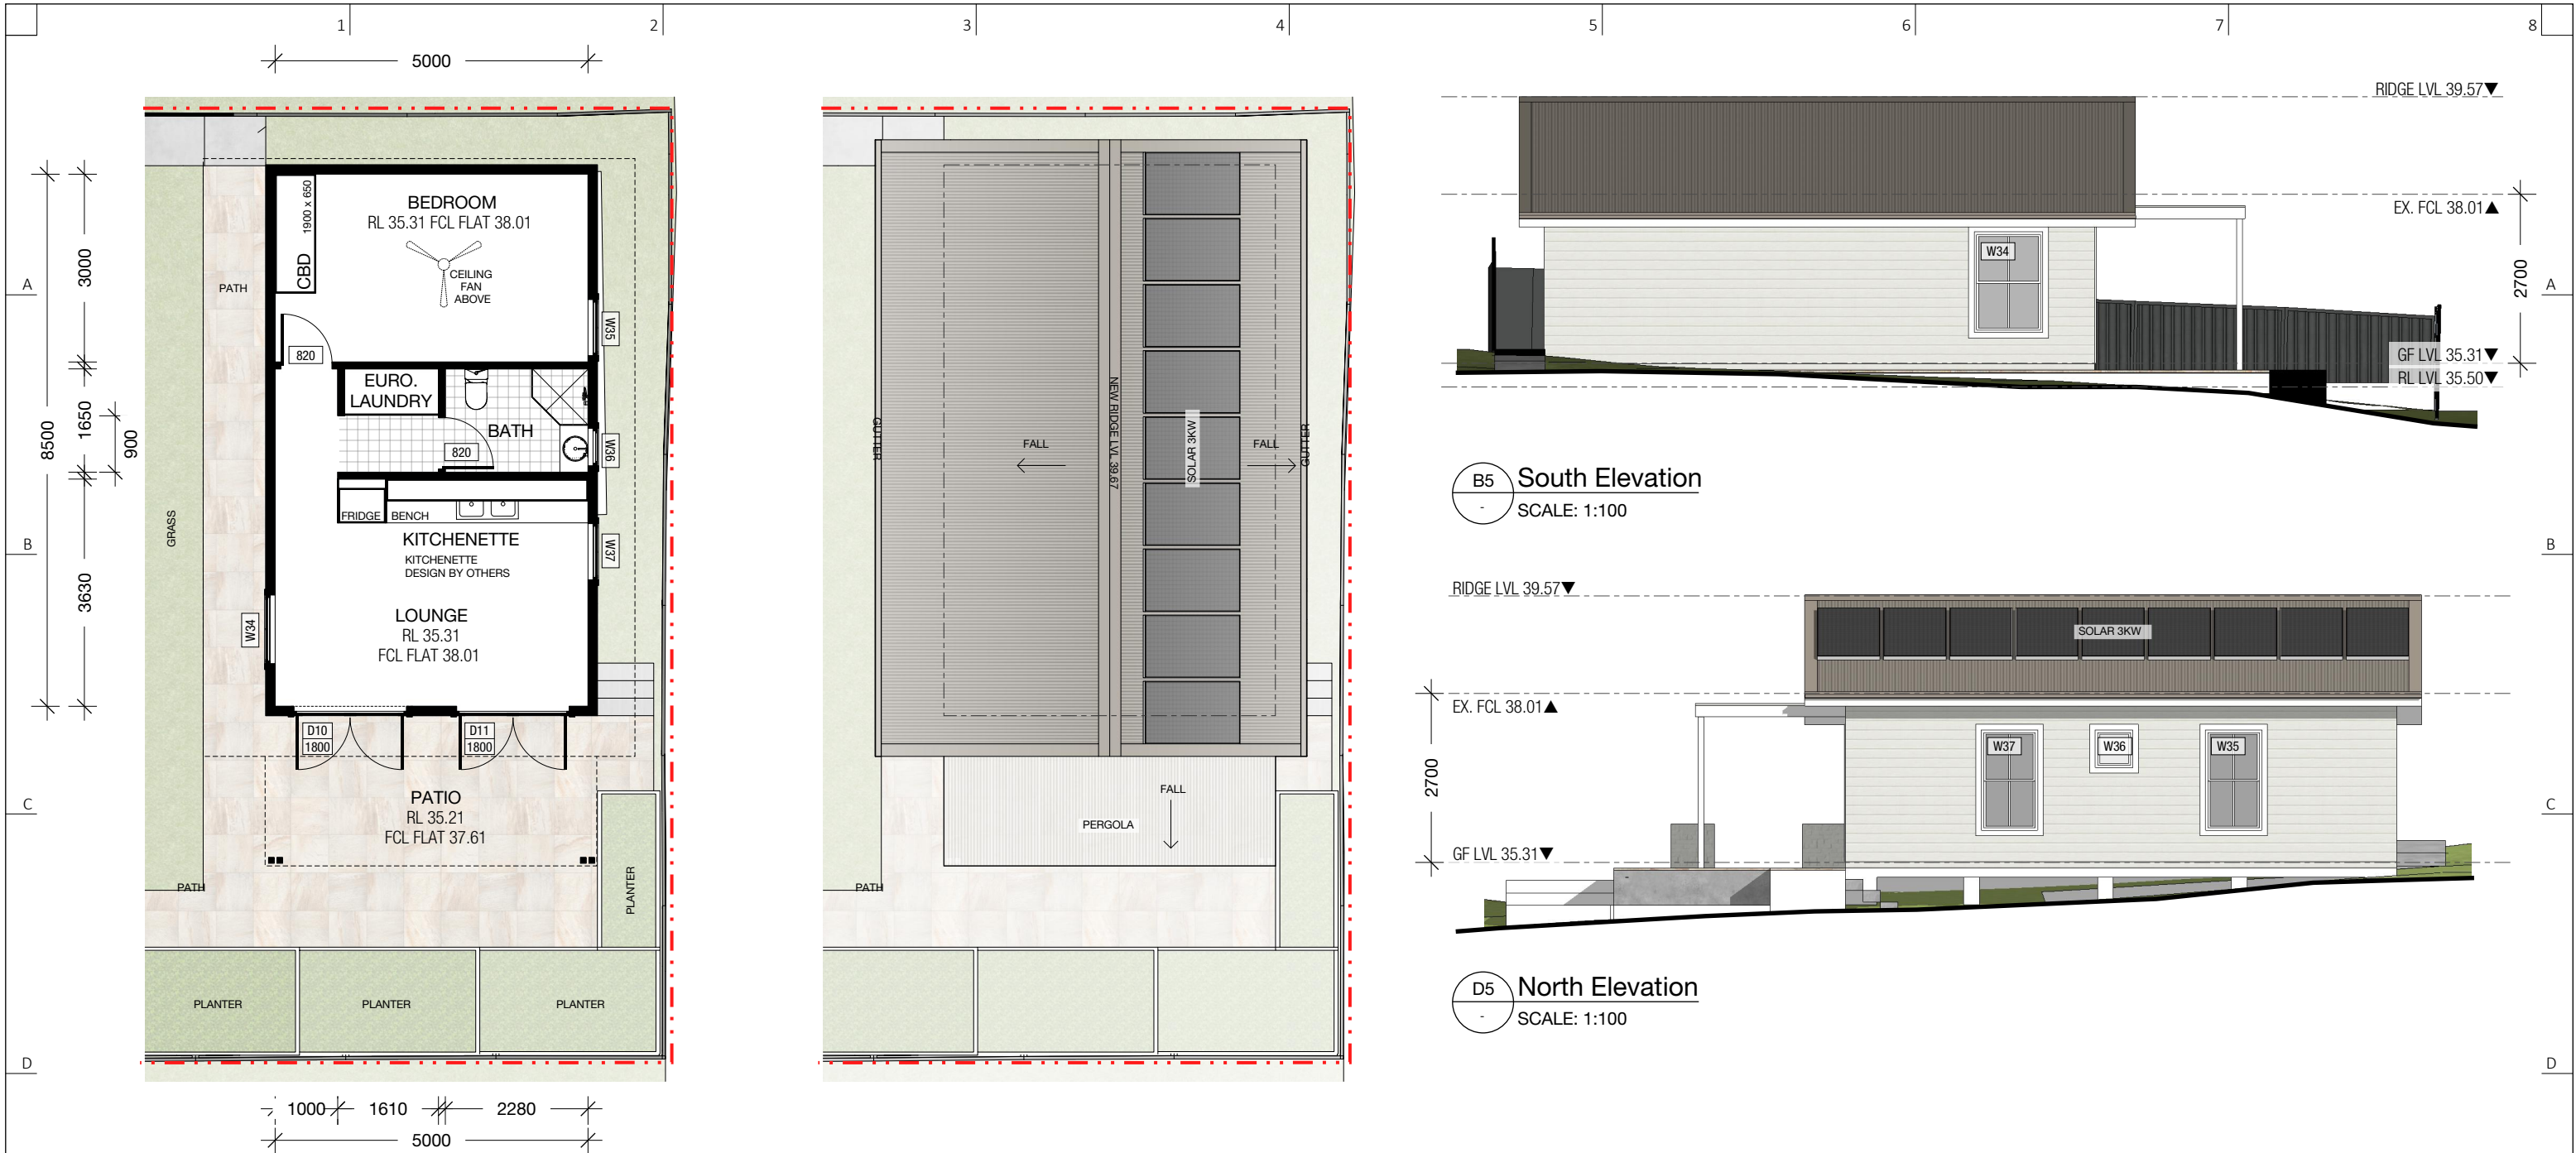


BUILDING DESIGN
INTERIOR DESIGN
PROJECT MANAGEMENT
DEVELOPMENT APPROVALS

www.emvy.com.au
design@emvy.com.au
0492 924 763
+612 4283 2685


North

ISSUE No DA DA	DESCRIPTION DEVELOPMENT APPLICATION DA MODIFICATION	DRAWN BY MV MV	CHECKED BY CA CA	DATE 25/02/26 25/05/26	NOTE TO BUILDER Figured dimensions shall be used. Do not scale drawing. The contractor shall verify all dimensions on site prior to commencement of work. All work to comply with the National Code of Construction (NCC 2022) & Australia Standards.	CLIENT AGREEMENT As the client I have read and approved all the drawings and specifications of the drawings. approved	CLIENT A & B CHRISTIE-DAVID PROJECT NAME ALTERATIONS & ADDITIONS PROJECT ADDRESS LOT 15 SEC M DP 2697 16 ALFRED STREET WOONONA NSW 2517	PROJECT # 186.25 SHEET NAME SECONDARY DWELLING SHEET NO. DA.A108 SCALE As noted @ A3 REVISION # -
----------------------	---	----------------------	------------------------	------------------------------	---	---	--	--


DO NOT USE THIS DRAWING FOR CONSTRUCTION UNLESS DESIGNATED

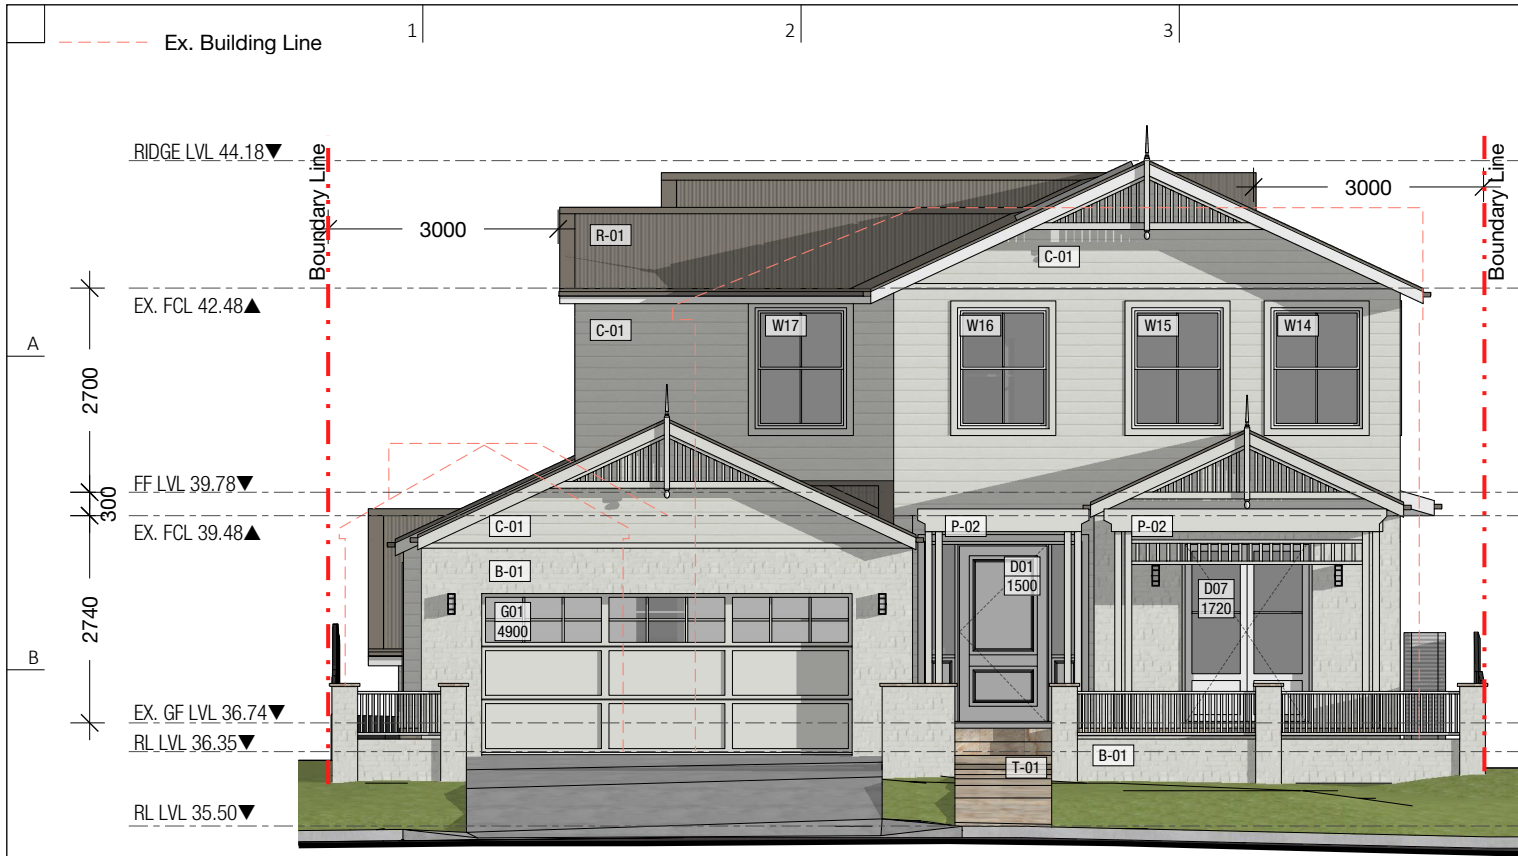

C1 South Elevation
SCALE: 1:100

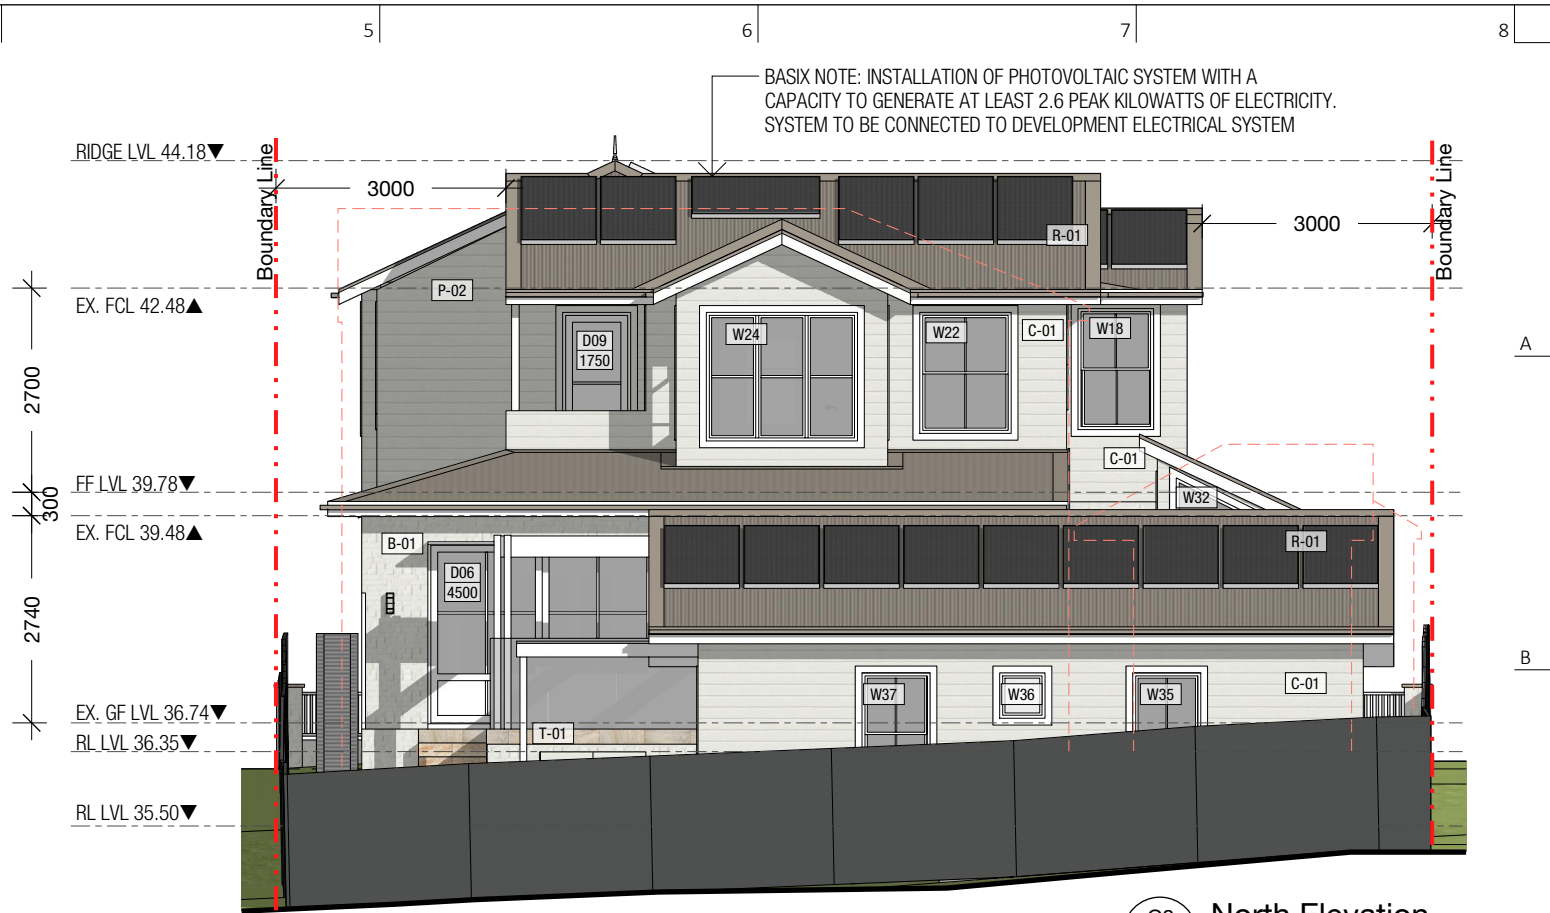

C8 North Elevation
SCALE: 1:100

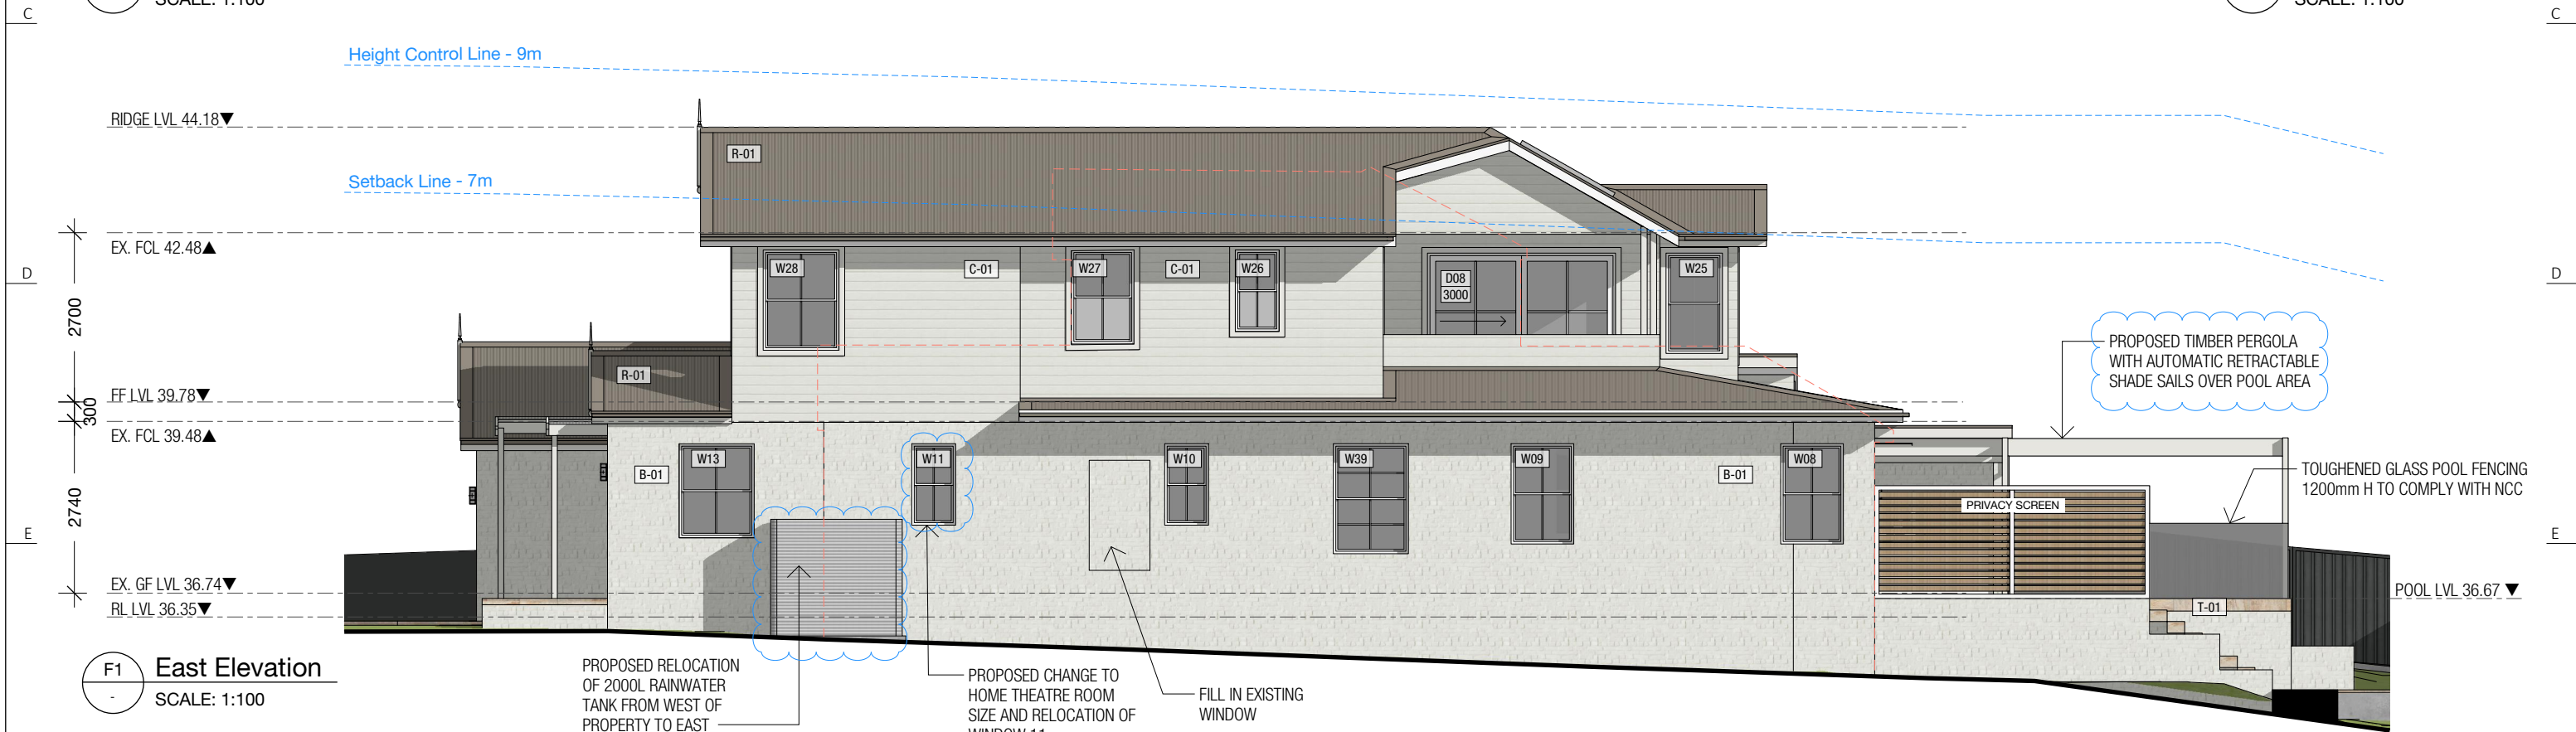


F1 East Elevation
SCALE: 1:100

DEVELOPMENT APPLICATION MODIFICATION


DO NOT USE THIS DRAWING FOR CONSTRUCTION UNLESS DESIGNATED

 BUILDING DESIGN INTERIOR DESIGN PROJECT MANAGEMENT DEVELOPMENT APPROVALS  ACCREDITED BUILDING DESIGNER www.emvy.com.au design@emvy.com.au 0492 924 763 +612 4283 2685	North	ISSUE No DA DA	DESCRIPTION DEVELOPMENT APPLICATION DA MODIFICATION	DRAWN BY MV MV	CHECKED BY CA CA	DATE 25/02/26 25/05/26	NOTE TO BUILDER Figured dimensions shall be used. Do not scale drawing. The contractor shall verify all dimensions on site prior to commencement of work. All work to comply with the National Code of Construction (NCC 2022) & Australia Standards.	CLIENT AGREEMENT As the client I have read and approved all the drawings and specifications of the drawings. approved	CLIENT A & B CHRISTIE-DAVID PROJECT NAME ALTERATIONS & ADDITIONS PROJECT ADDRESS LOT 15 SEC M DP 2697 16 ALFRED STREET WOONONA NSW 2517	PROJECT # 186.25 SCALE As noted @ A3 SHEET NAME E & N ELEVATIONS SHEET NO. DA.A200 REVISION # 1
--	-------	----------------------	---	----------------------	------------------------	------------------------------	---	---	--	--

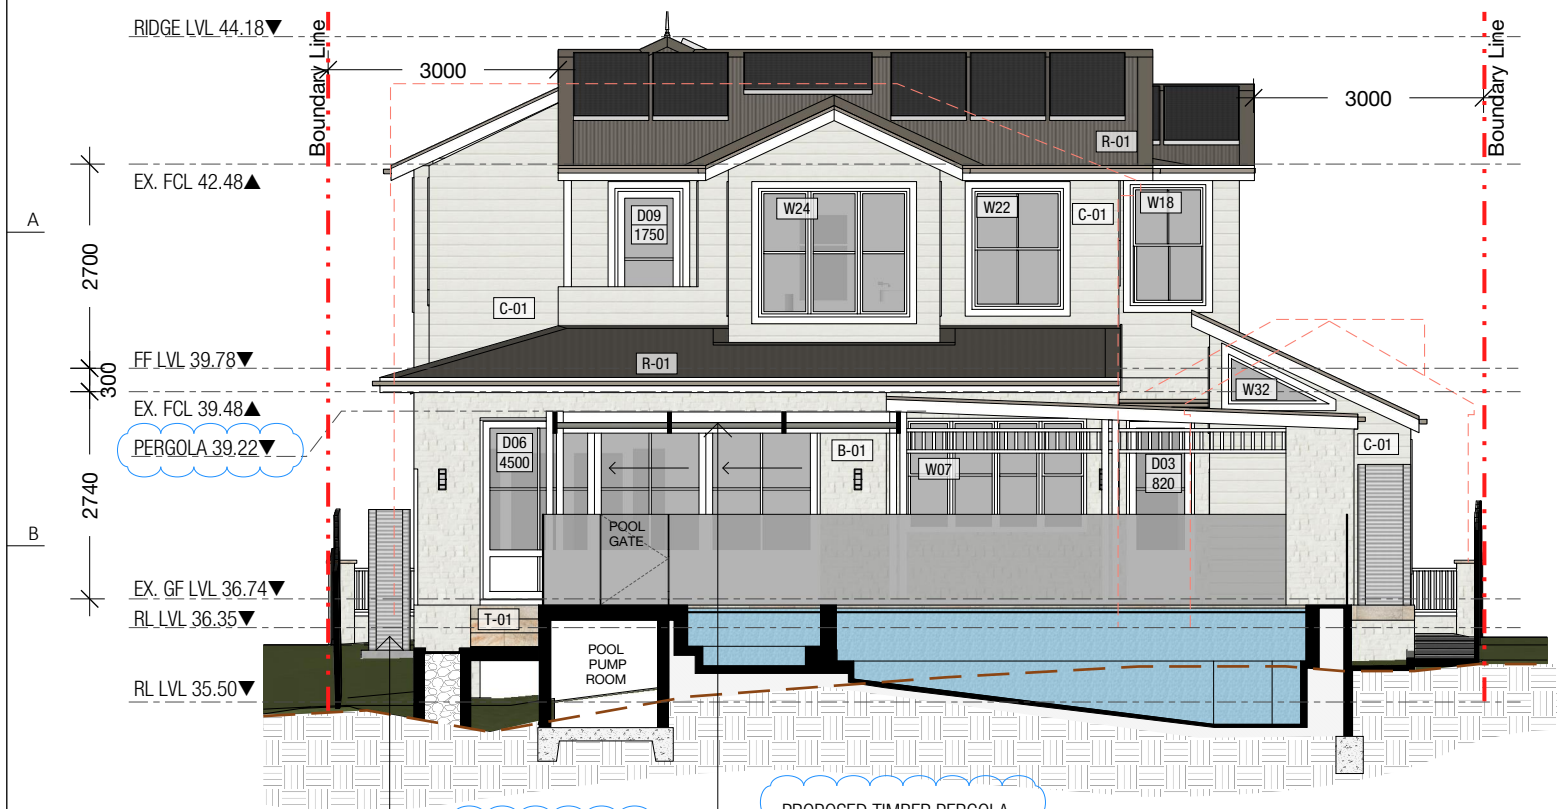

C1 North Elevation
SCALE: 1:100



FINISHES SCHEDULE			
P-01		PAINT FINISH (EXISTING CLADDING & RENDER)	DULUX: SNOWY MOUNTAINS
P-02		PAINT FINISH (POSTS BEAMS & TRIM)	DULUX CASPER WHITE QUARTER
C-01		NEW EXTERNAL WALL CLADDING AND PAINTED P-01	JAMES HARDIE Linea Weatherboard - 150mm Paint Finish P-01
B-01		BRICKS RENDERED AND PAINTED P-01	COMMON BRICK
R-01		ROOFING MATERIALS	COLORBOND - GULLY
T-01		LANDSCAPE TILE/PAVER	TBC

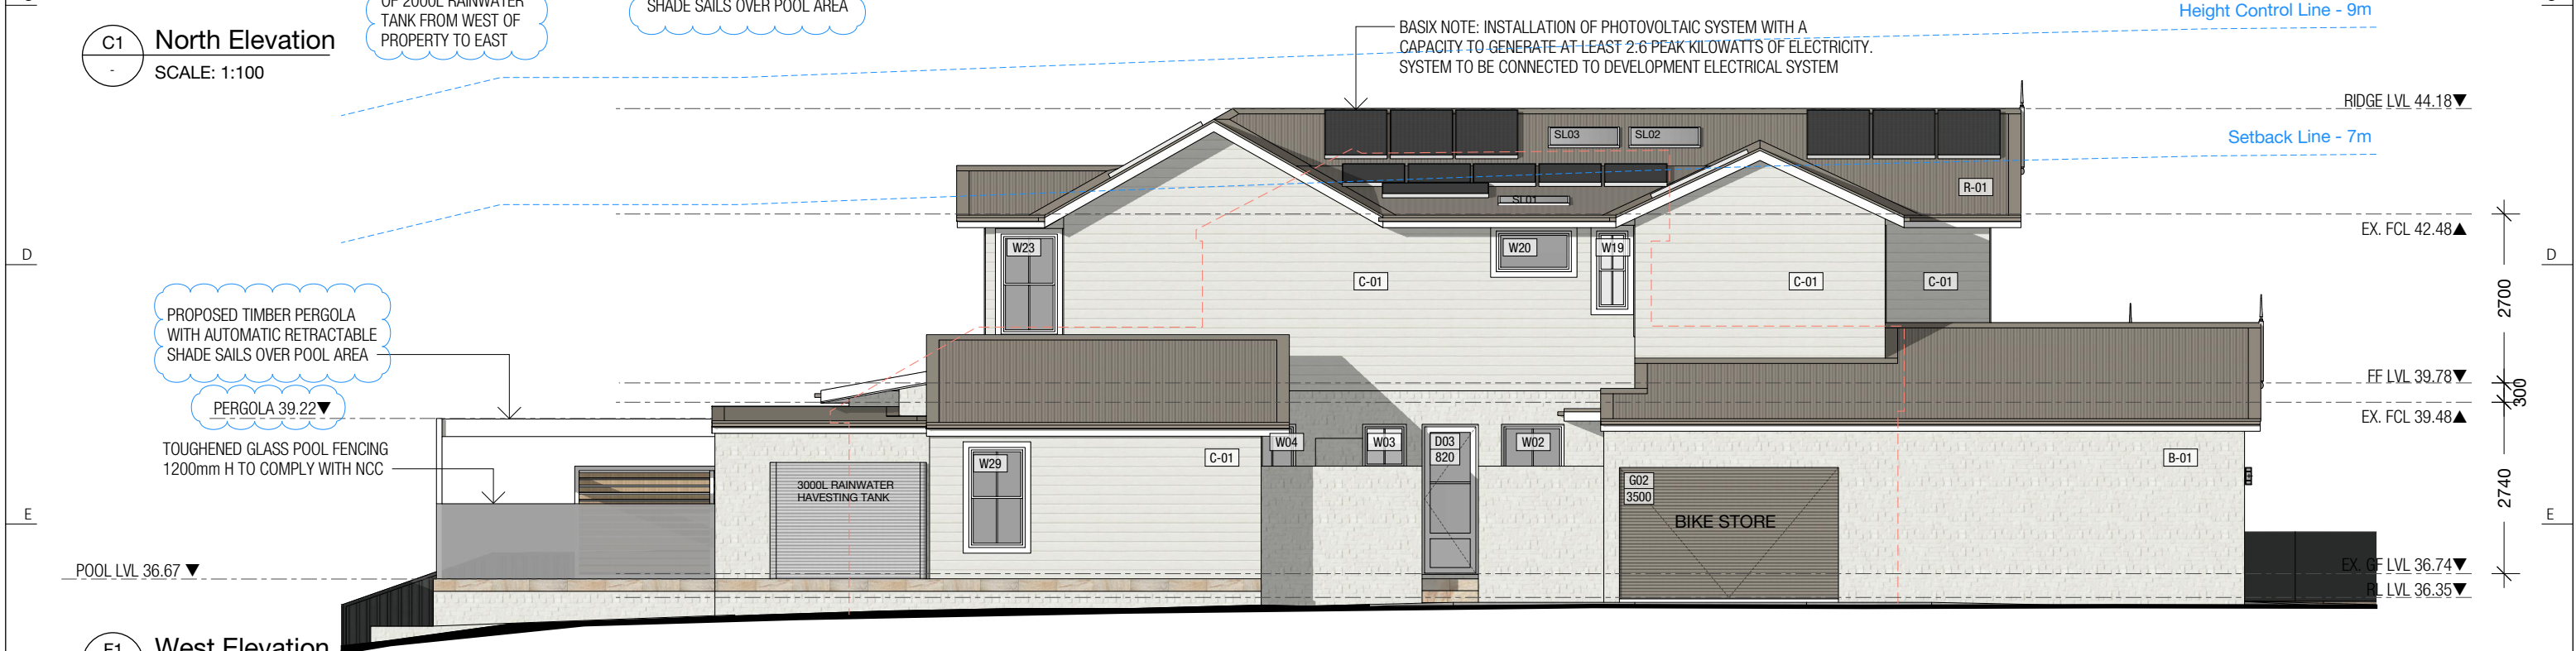

F1 West Elevation
SCALE: 1:100

DEVELOPMENT APPLICATION MODIFICATION

DO NOT USE THIS DRAWING FOR CONSTRUCTION UNLESS DESIGNATED

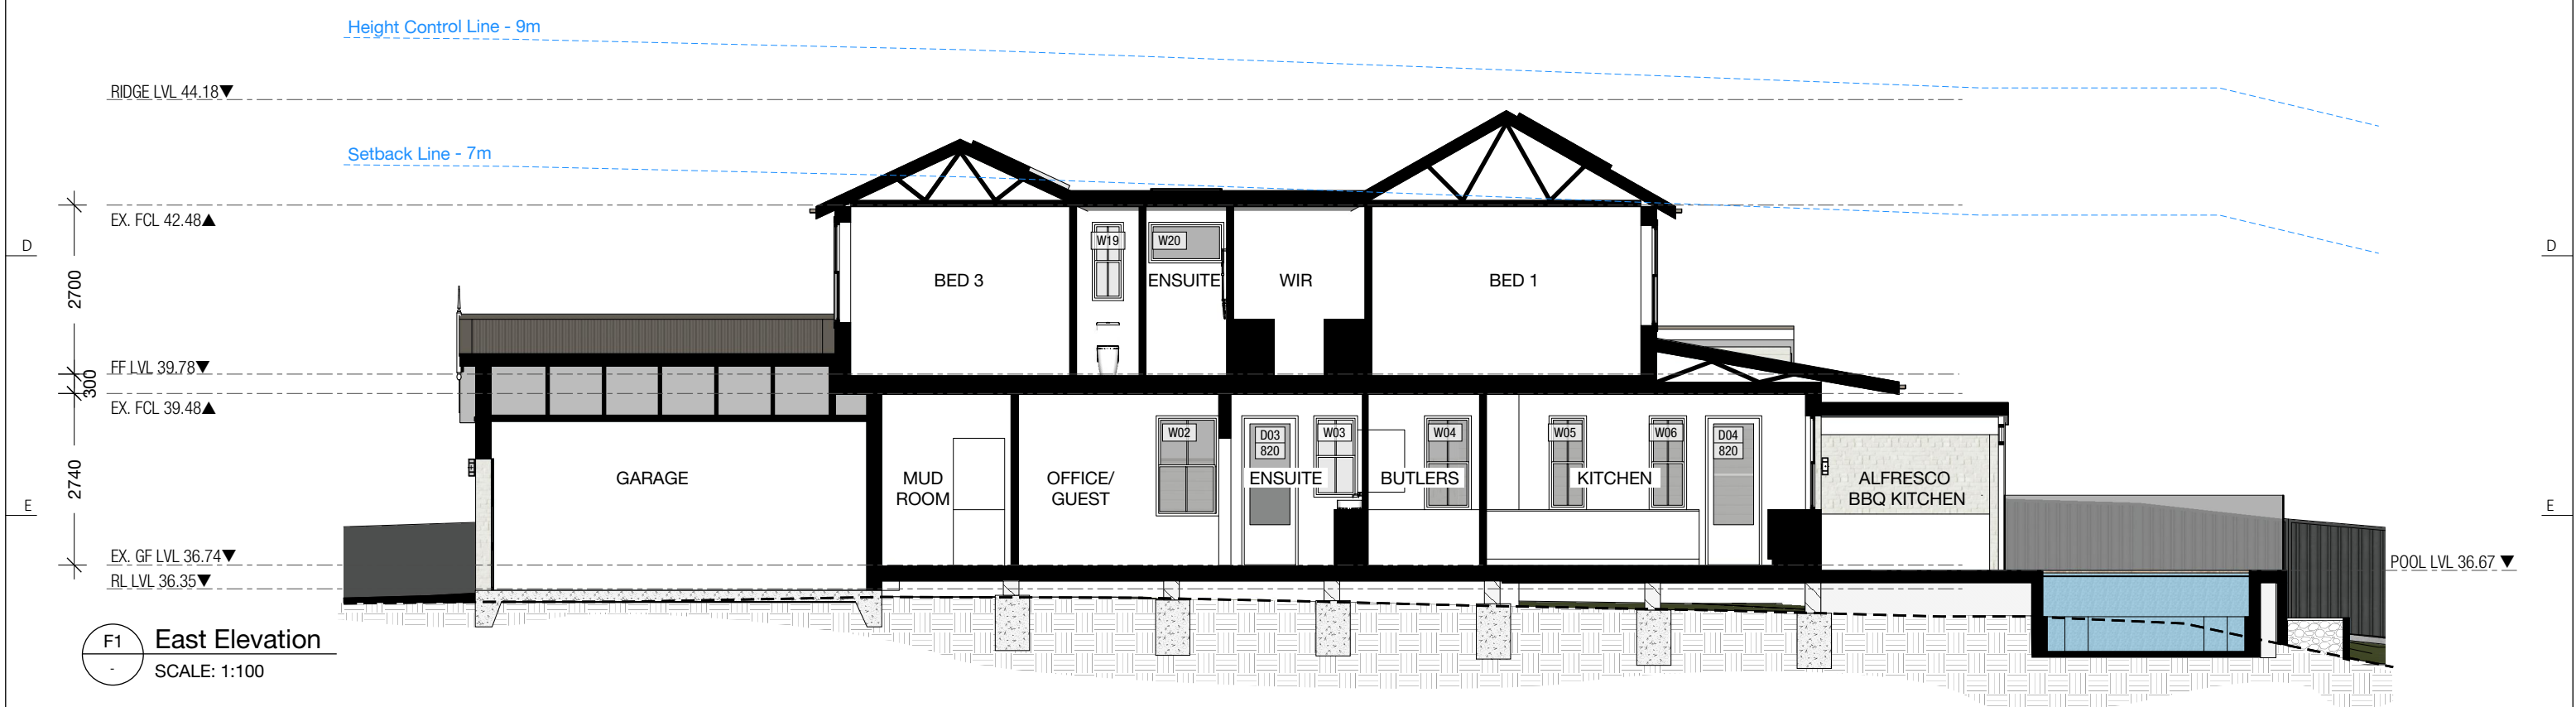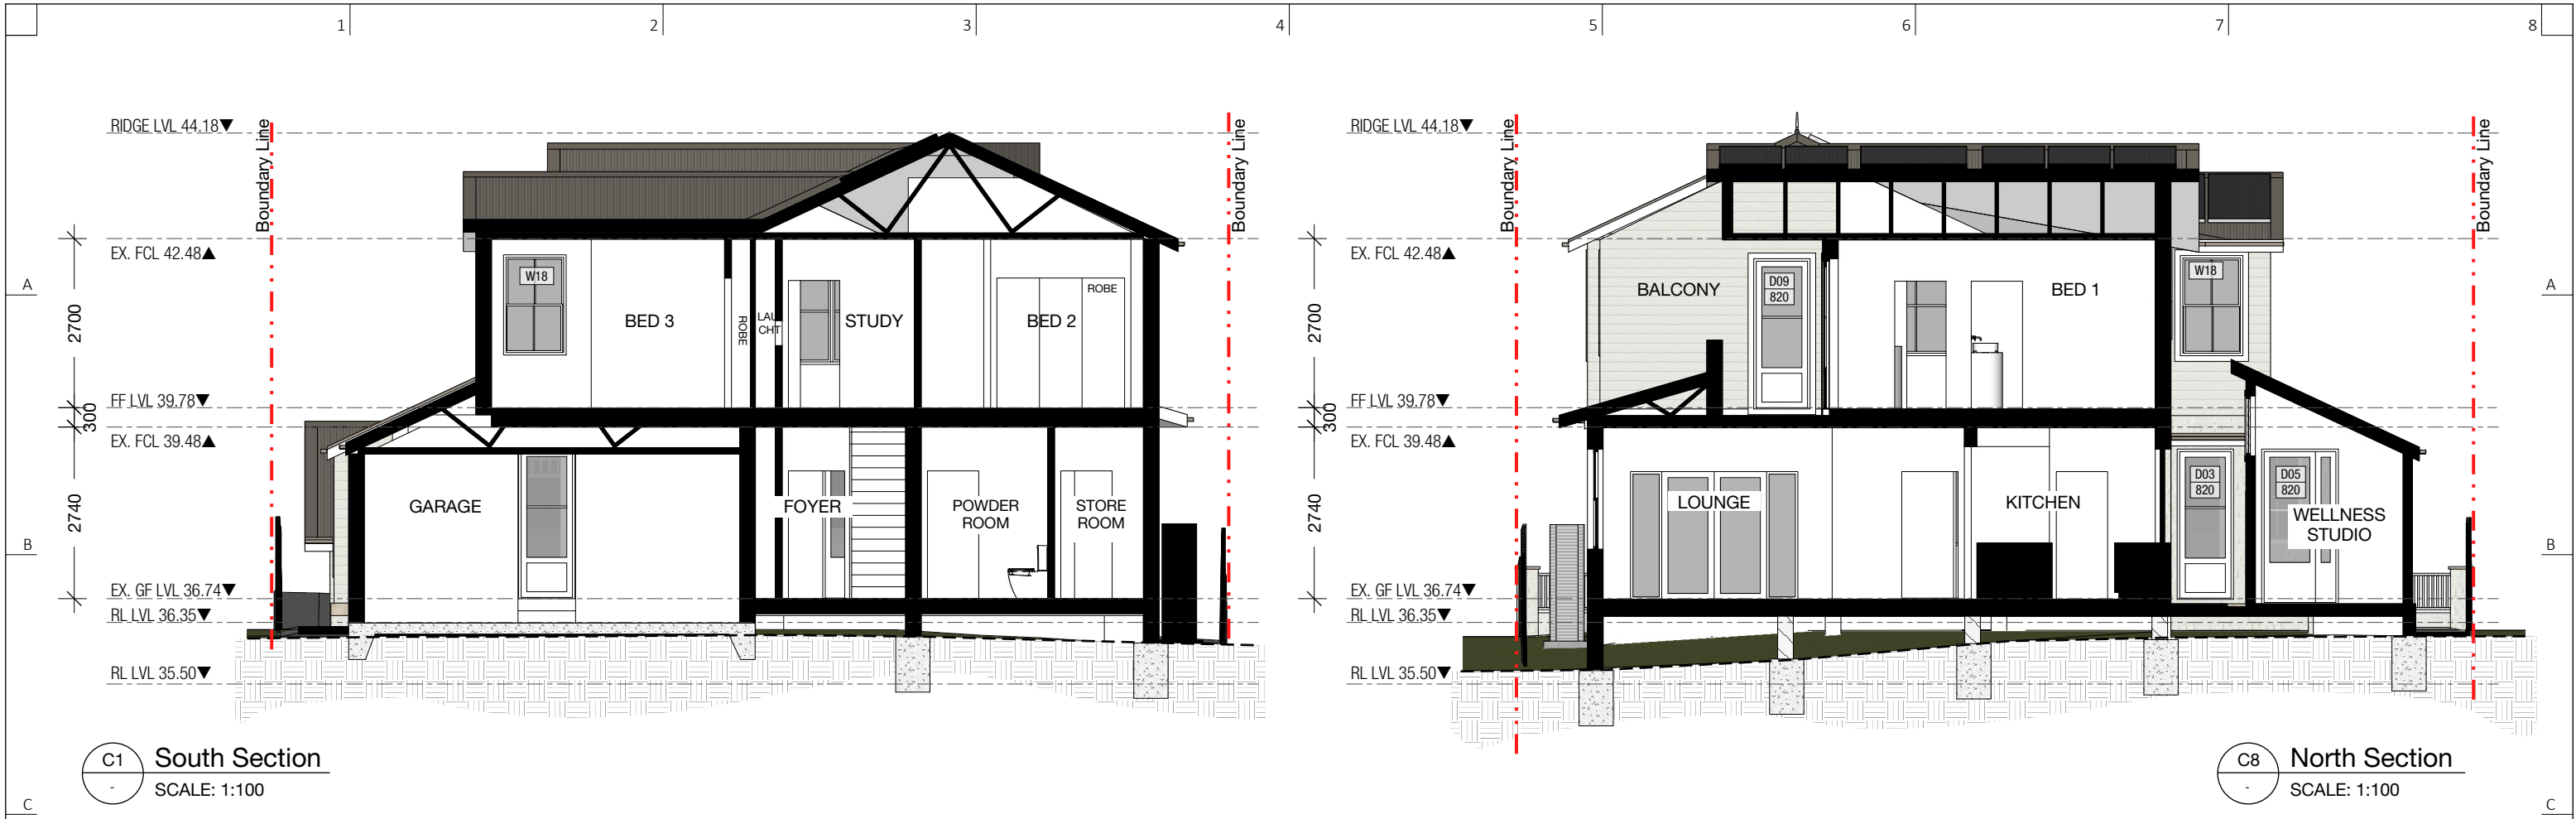


DEVELOPMENT APPLICATION MODIFICATION

DO NOT USE THIS DRAWING FOR CONSTRUCTION UNLESS DESIGNATED

				www.emvy.com.au design@emvy.com.au 0492 924 763 +612 4283 2685		North	ISSUE No DA DA	DESCRIPTION DEVELOPMENT APPLICATION DA MODIFICATION	DRAWN BY MV MV	CHECKED BY CA CA	DATE 25/02/26 25/05/26	NOTE TO BUILDER Figured dimensions shall be used. Do not scale drawing. The contractor shall verify all dimensions on site prior to commencement of work. All work to comply with the National Code of Construction (NCC 2022) & Australia Standards.	CLIENT AGREEMENT As the client I have read and approved all the drawings and specifications of the drawings. approved	CLIENT A & B CHRISTIE-DAVID PROJECT NAME ALTERATIONS & ADDITIONS PROJECT ADDRESS LOT 15 SEC M DP 2697 16 ALFRED STREET WOONONA NSW 2517	PROJECT # 186.25 SHEET NAME S - E - N SECTIONS SHEET NO. DA. A300	SCALE As noted @ A3 REVISION # 1
--	--	--	--	---	--	-------	----------------------	---	----------------------	------------------------	------------------------------	---	---	--	--	---



C1 West Section
SCALE: 1:100

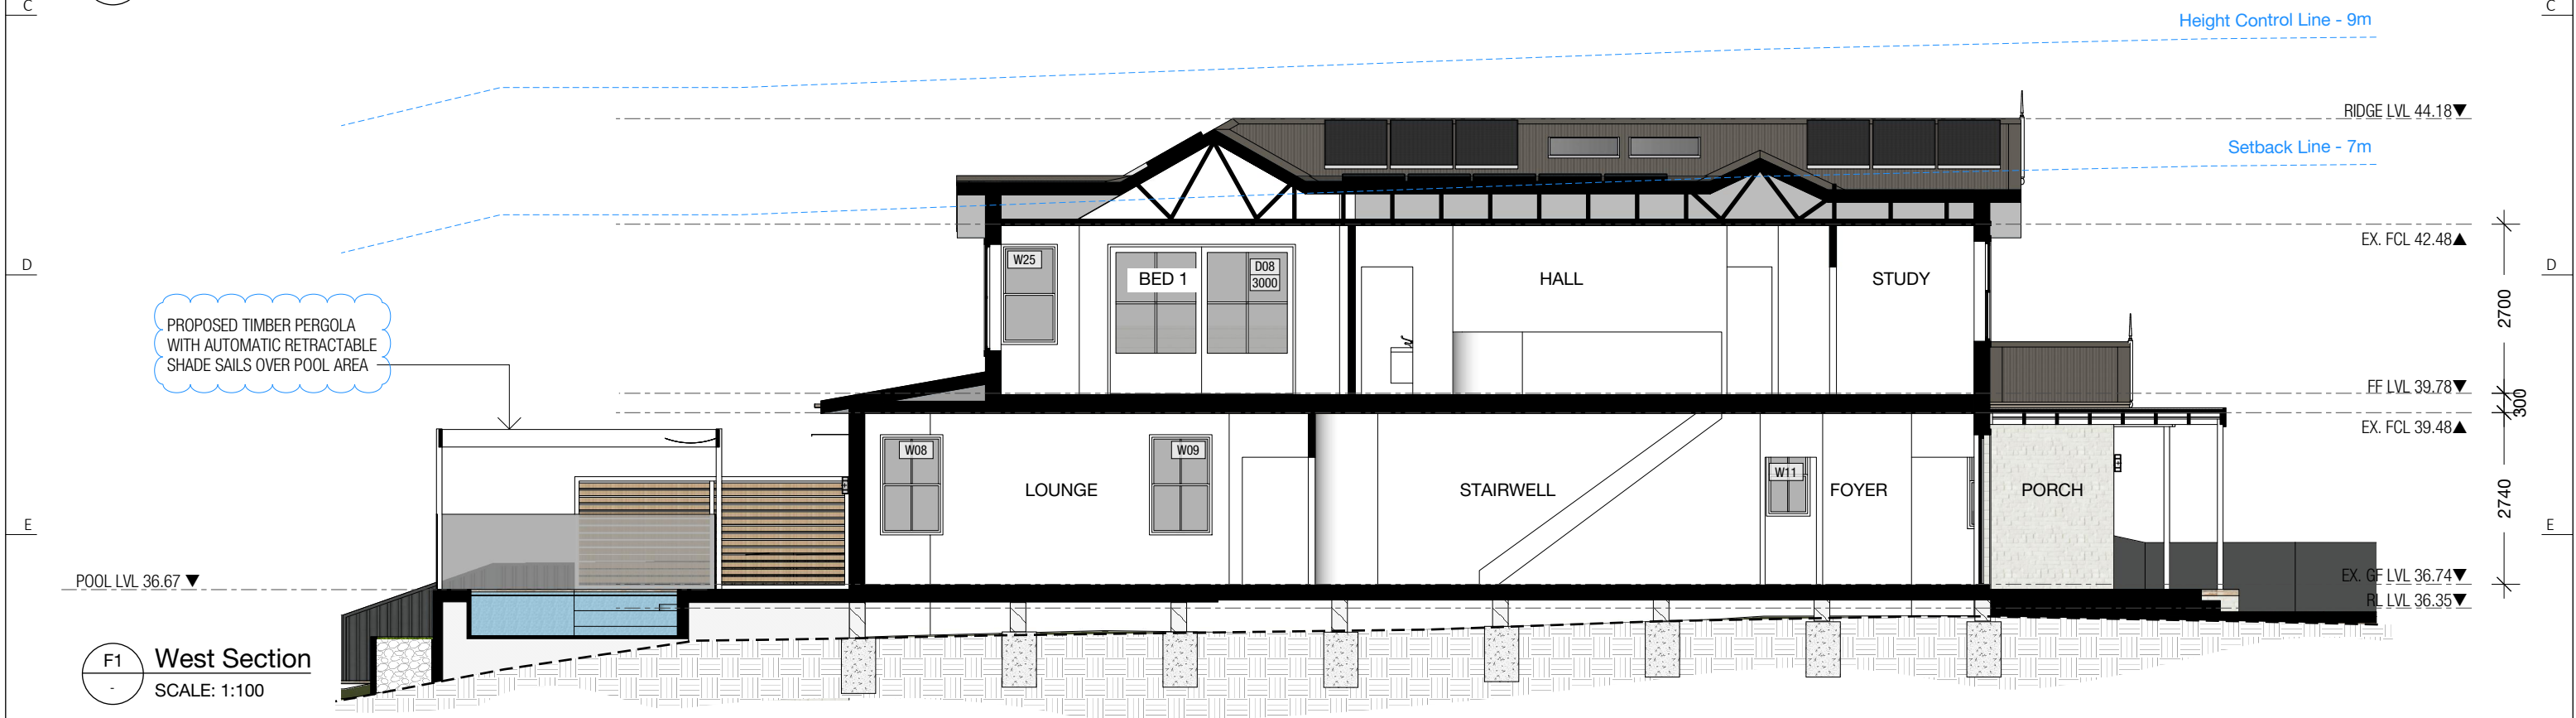


F1 West Section
SCALE: 1:100

DEVELOPMENT APPLICATION MODIFICATION


DO NOT USE THIS DRAWING FOR CONSTRUCTION UNLESS DESIGNATED

 BUILDING DESIGN INTERIOR DESIGN PROJECT MANAGEMENT DEVELOPMENT APPROVALS			 www.emvy.com.au design@emvy.com.au 0492 924 763 +612 4283 2685			North	ISSUE No DA DA	DESCRIPTION DEVELOPMENT APPLICATION DA MODIFICATION	DRAWN BY MV MV	CHECKED BY CA CA	DATE 25/02/26 25/05/26	NOTE TO BUILDER Figured dimensions shall be used. Do not scale drawing. The contractor shall verify all dimensions on site prior to commencement of work. All work to comply with the National Code of Construction (NCC 2022) & Australia Standards.	CLIENT AGREEMENT As the client I have read and approved all the drawings and specifications of the drawings. approved	CLIENT A & B CHRISTIE-DAVID PROJECT NAME ALTERATIONS & ADDITIONS PROJECT ADDRESS LOT 15 SEC M DP 2697 16 ALFRED STREET WOONONA NSW 2517	PROJECT # 186.25 SHEET NAME W SECTIONS SHEET NO. DA.A301	SCALE As noted @ A3 REVISION # 1
--	--	--	---	--	--	-------	----------------------	---	----------------------	------------------------	------------------------------	---	---	--	---	---


GROUND FLOOR WINDOWS

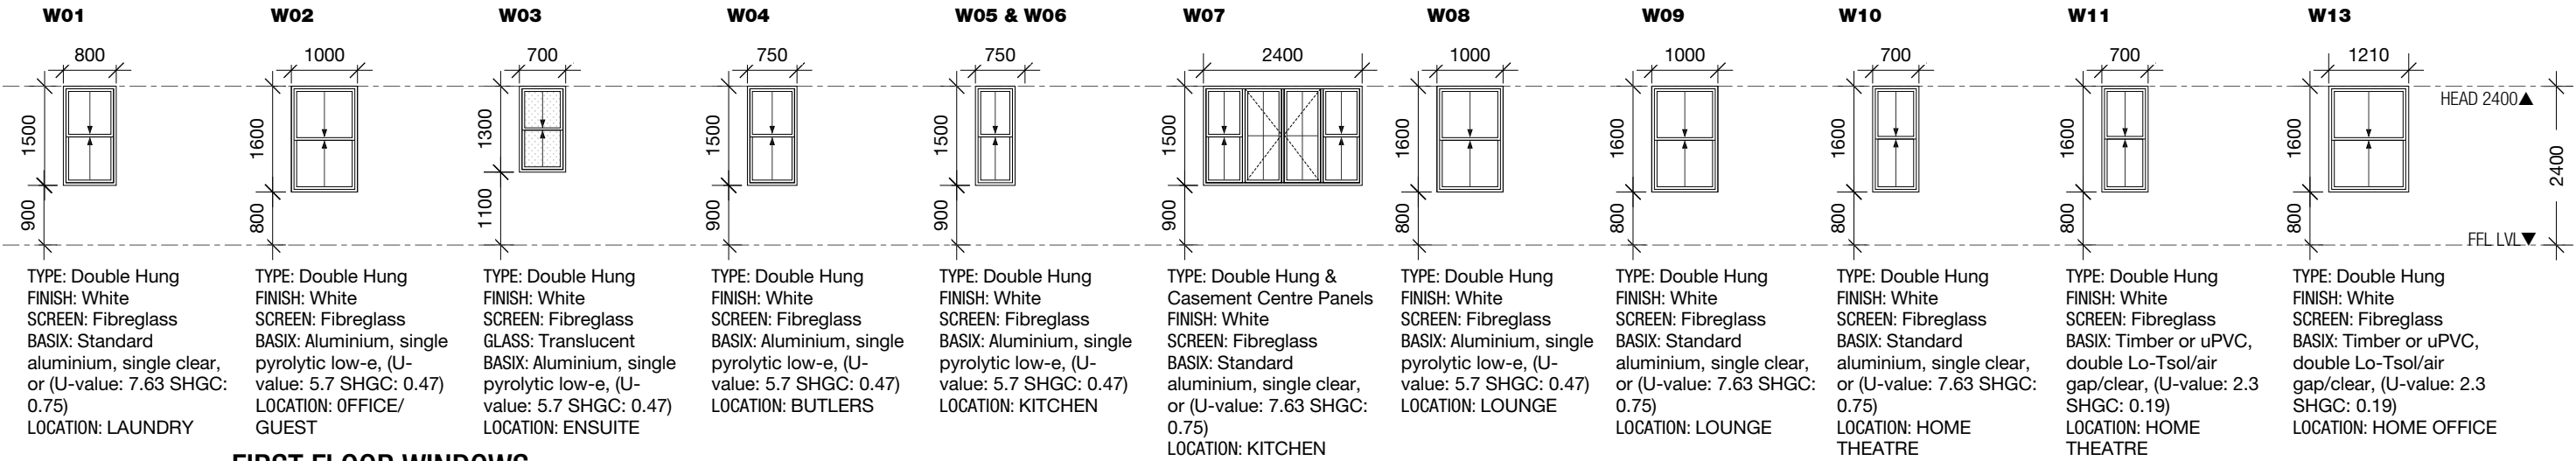

FIRST FLOOR WINDOWS

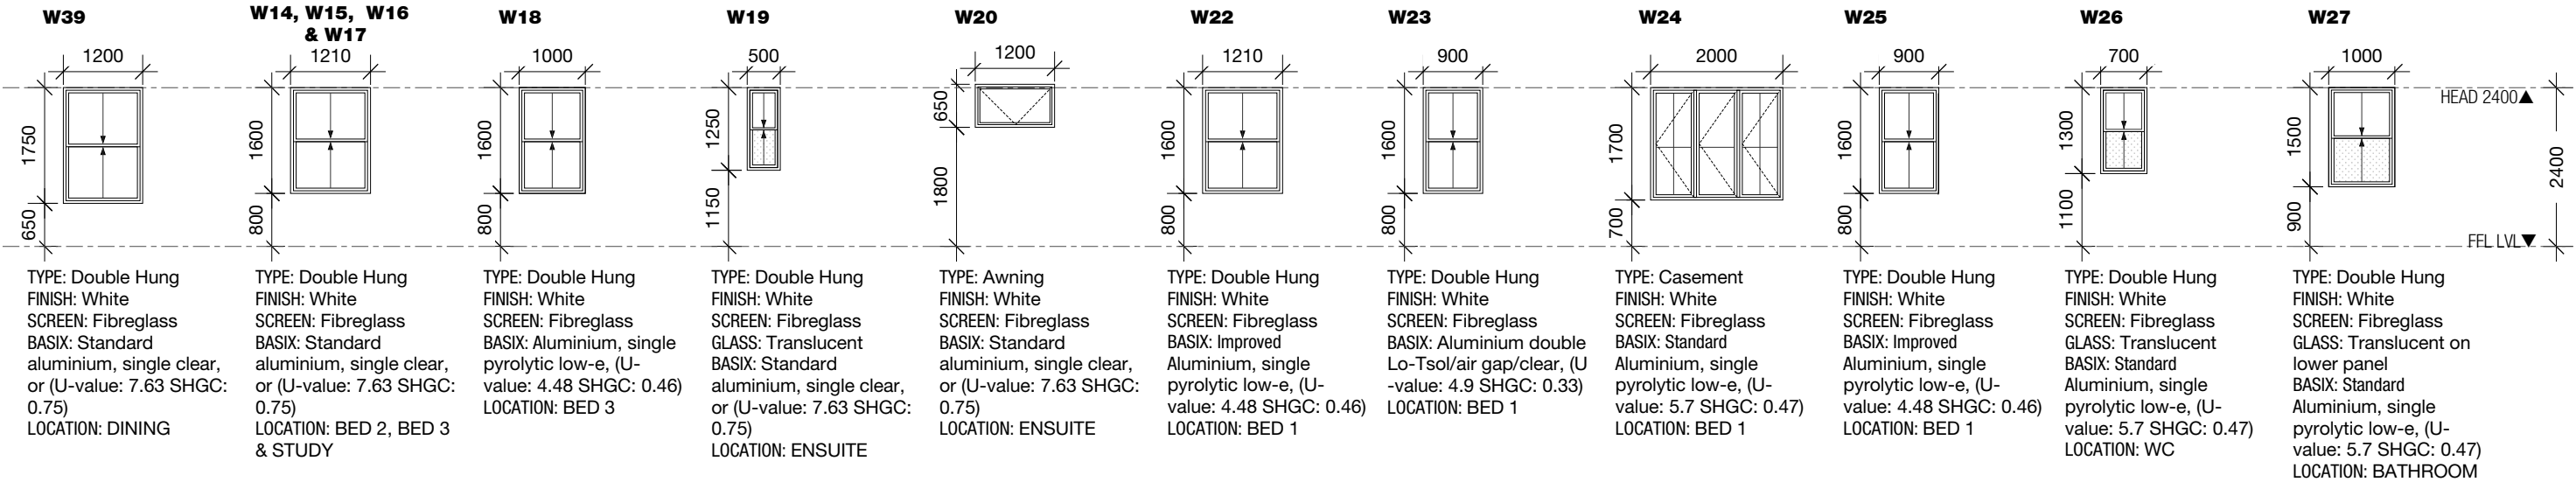

GROUND FLOOR DOORS

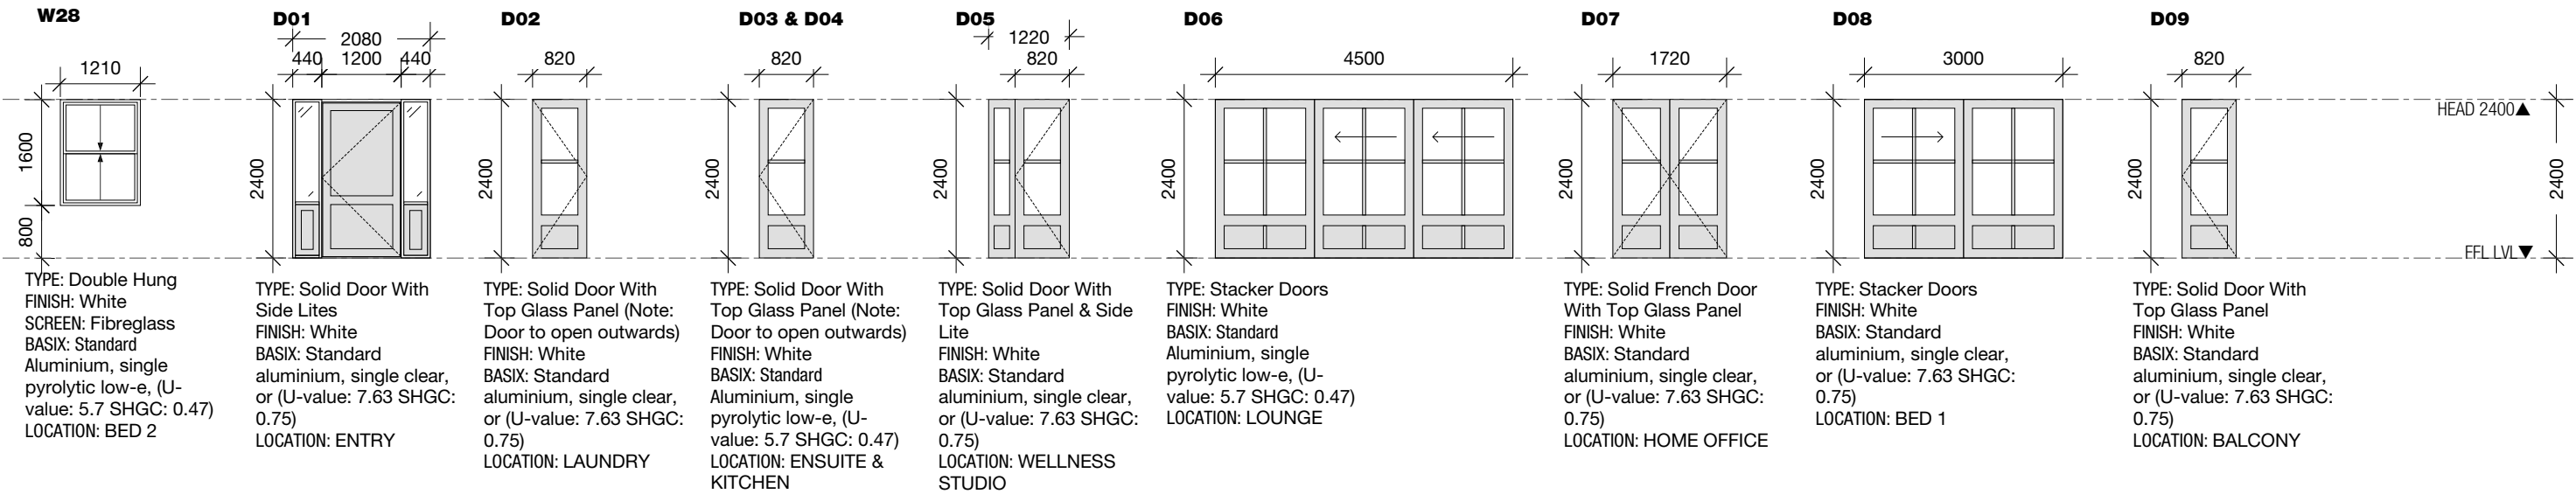

DEVELOPMENT APPLICATION MODIFICATION

DO NOT USE THIS DRAWING FOR CONSTRUCTION UNLESS DESIGNATED



BUILDING DESIGN
INTERIOR DESIGN
PROJECT MANAGEMENT
DEVELOPMENT APPROVALS



www.emvy.com.au
design@emvy.com.au
0492 924 763
+612 4283 2685

North

ISSUE No
DA
DA

DESCRIPTION
DEVELOPMENT APPLICATION
DA MODIFICATION

DRAWN BY
MV
MV

CHECKED BY
CA
CA

DATE
25/02/26
25/05/26

NOTE TO BUILDER
Figured dimensions shall be used.
Do not scale drawing.
The contractor shall verify all dimensions on site prior to commencement of work.
All work to comply with the National Code of Construction (NCC 2022) & Australia Standards.

CLIENT AGREEMENT
As the client I have read and approved all the drawings and specifications of the drawings.

approved

CLIENT
A & B CHRISTIE-DAVID
PROJECT NAME
ALTERATIONS & ADDITIONS
PROJECT ADDRESS
LOT 15 SEC M DP 2697
16 ALFRED STREET
WOONONA NSW 2517


PROJECT #
186.25

SCALE
As noted @ A3


SHEET NAME
WINDOW & DOOR SCHEDULE
SHEET NO.
DA. A500

REVISION #
-



WELLNESS STUDIO WINDOWS

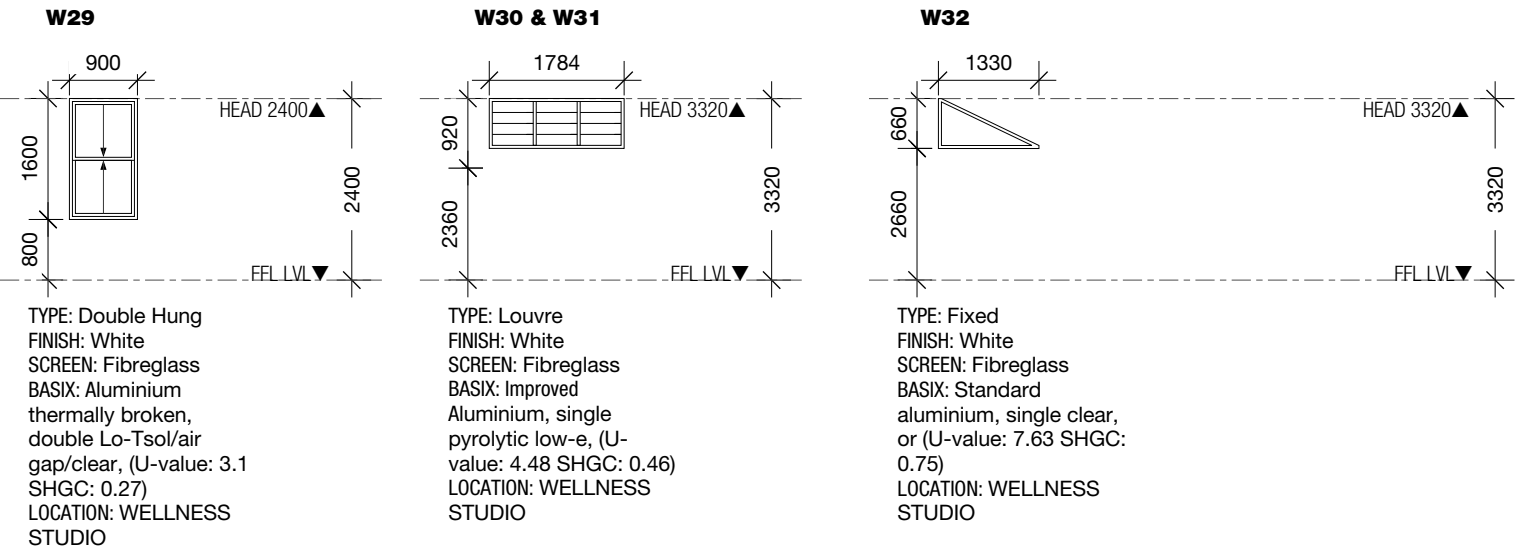

SKYLIGHTS

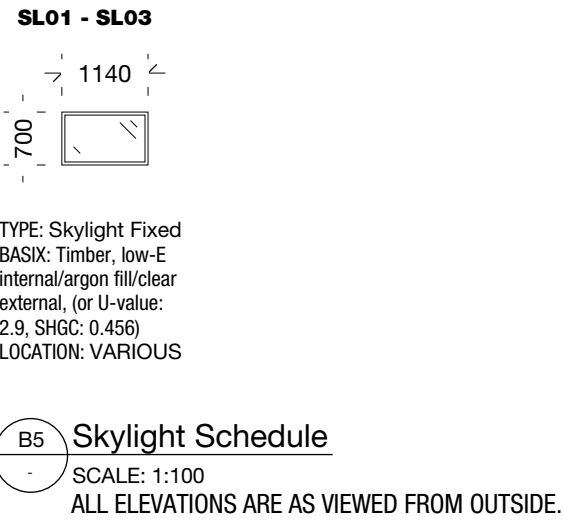

SECONDARY DWELLING

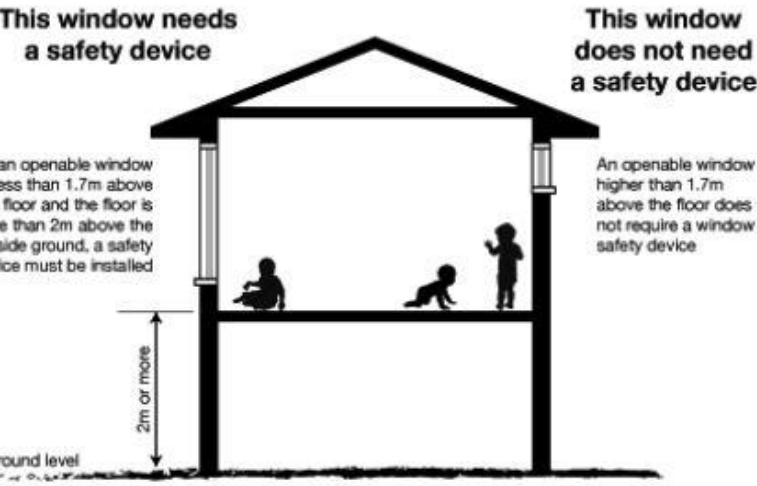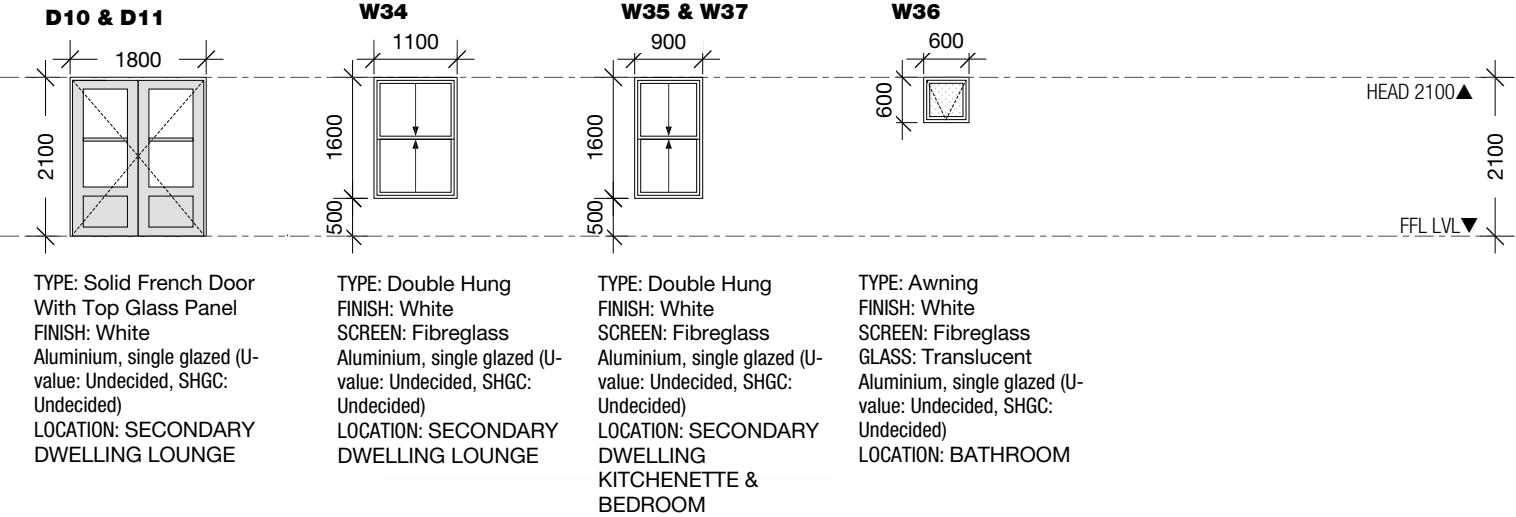

BASIX NOTES CERTIFICATE NUMBER: ---

GLAZING REQUIREMENT
WINDOWS AND GLAZED DOORS

- The applicant must install the windows, glazed doors and shading devices, in accordance with the specifications listed in the table below. Relevant overshadowing specifications must be satisfied for each window and glazed door.
- For projections described in millimetres, the leading edge of each eave, pergola, verandah, balcony or awning must be no more than 500 mm above the head of the window or glazed door and no more than 2400 mm above the sill.
- Overshadowing buildings or vegetation must be of the height and distance from the centre and the base of the window and glazed door, as specified in the 'overshadowing' column in the table below.

SKYLIGHTS

- The applicant must install the skylights in accordance with the specifications listed in the table below.

PROTECTION OF OPENABLE WINDOWS
WINDOWS WITH SILL HEIGHTS IN BEDROOMS LESS THAN 1.7M MUST BE-

- FITTED WITH SCREENS OR DEVICES THAT RESTRICT THE OPENING SUCH THAT A 125MM SPHERE CANNOT PASS THROUGH THE OPENING OR SCREEN;
- THE DEVICE/SCREEN MUST BE CAPABLE OF RESISTING OUTWARD HORIZONTAL ACTION OF 250N;
- THE DEVICE OR SCREEN MUST BE A PERMANENT FIXTURE;

NOTE: IF WINDOW LIMITERS ARE EMPLOYED FOR PROTECTION, THE VENTILATION REQUIREMENTS OF PART 3.8.5 REMAIN APPLICABLE.


WINDOW & DOOR NOTES
ANY CHANGES FROM DRAWINGS TO BE CONFIRMED WITH DESIGNER PRIOR TO CONSTRUCTION. FABRICATOR TO CONFIRM LATEST DRAWING ISSUE PRIOR TO CONSTRUCTION. ANY INCONSISTANCIES IN DRAWINGS OR WINDOW DESIGN ISSUES TO BE REPORTED TO DESIGNER PRIOR TO CONSTRUCTION.

ALL GLAZING TO COMPLY WITH AS1288
ALL WINDOWS AND DOORS DRAWN FROM OUTSIDE
ALL DIMENSIONS TO BE CONFIRMED ON SITE BY FABRICATOR
ALL GROUND FLOOR WINDOWS TO HAVE LOCKING HARDWARE

DEVELOPMENT APPLICATION MODIFICATION

LEGEND

- Boundary Line
- Second Storey
- 21st June - 9AM
- 21st June - 12PM
- 21st June - 3PM

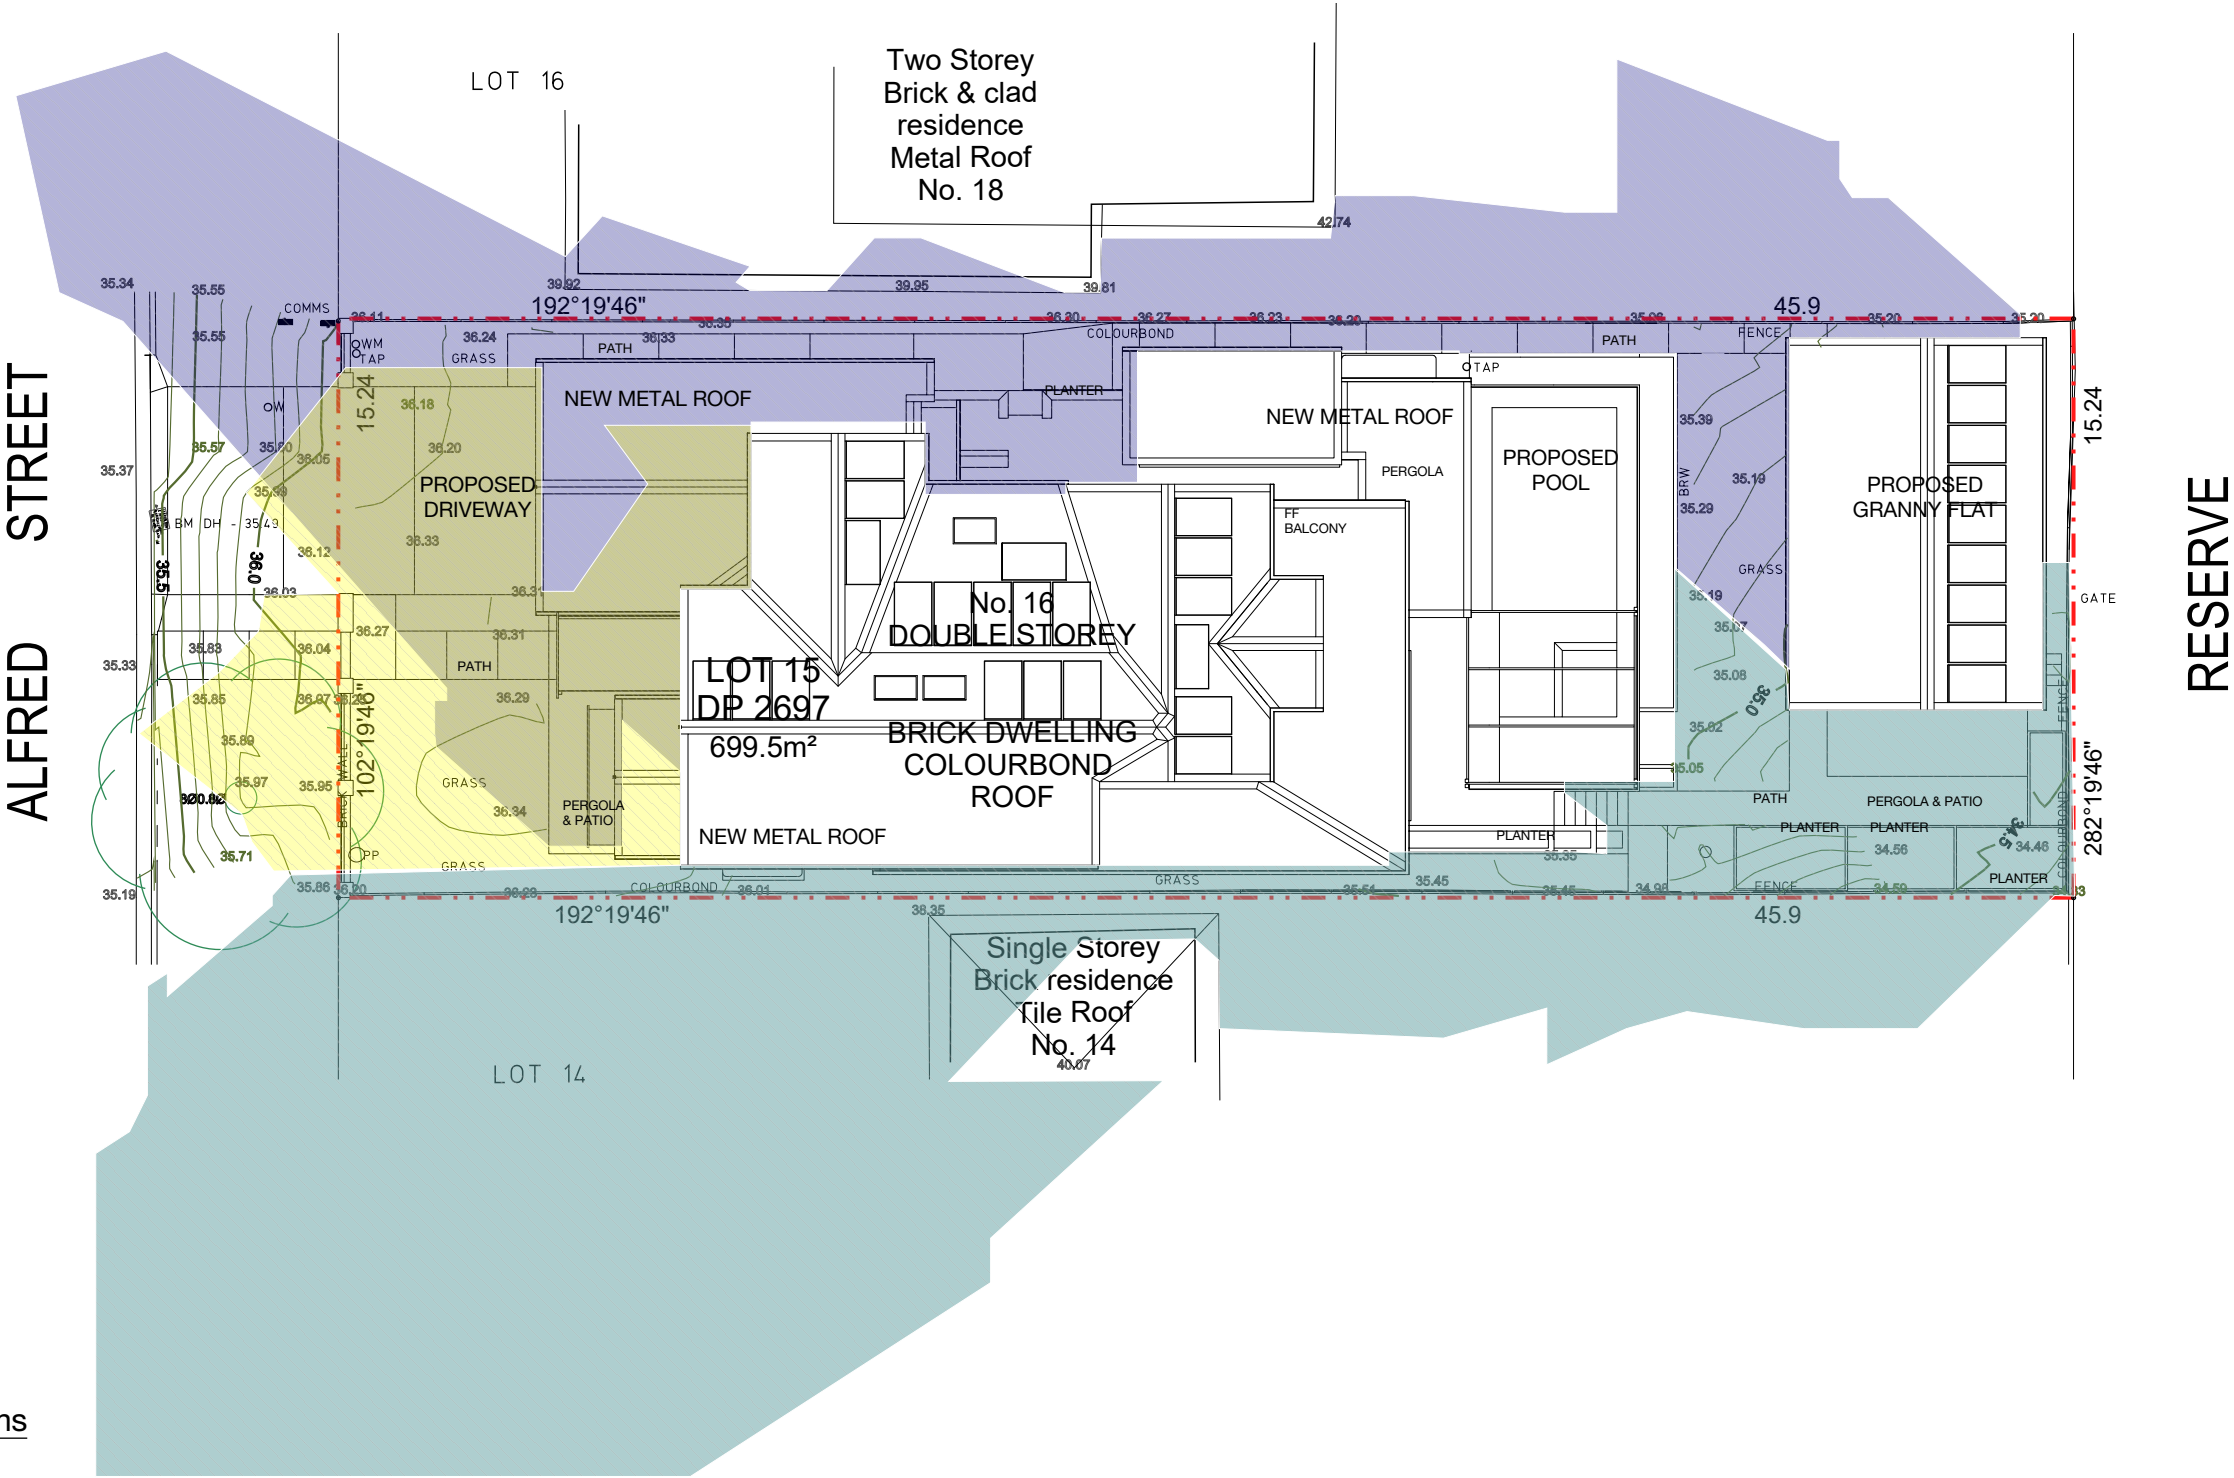

01 Shadow Diagrams
SCALE: 1:200

DEVELOPMENT APPLICATION MODIFICATION
DO NOT USE THIS DRAWING FOR CONSTRUCTION UNLESS DESIGNATED




BUILDING DESIGN
INTERIOR DESIGN
PROJECT MANAGEMENT
DEVELOPMENT APPROVALS



ACCREDITED
BUILDING DESIGNER

www.emvy.com.au
design@emvy.com.au
0492 924 763
+612 4283 2685

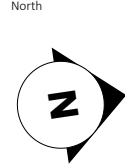

ISSUE No	DESCRIPTION	DRAWN BY	CHECKED BY	DATE
DA DA	DEVELOPMENT APPLICATION DA MODIFICATION	MV MV	CA CA	25/02/26 25/05/26


NOTE TO BUILDER
Figured dimensions shall be used.
Do not scale drawing.
The contractor shall verify all dimensions on site prior to commencement of work.
All work to comply with the National Code of Construction (NCC 2022) & Australia Standards.

CLIENT AGREEMENT
As the client I have read and approved all the drawings and specifications of the drawings.

approved



CLIENT
A & B CHRISTIE-DAVID
PROJECT NAME
ALTERATIONS & ADDITIONS
PROJECT ADDRESS
LOT 15 SEC M DP 2697
16 ALFRED STREET
WOONONA NSW 2517

PROJECT # 186.25	SCALE As noted @ A3
SHEET NAME SHADOW DIAGRAMS	REVISION #
SHEET NO. DA. A502	-

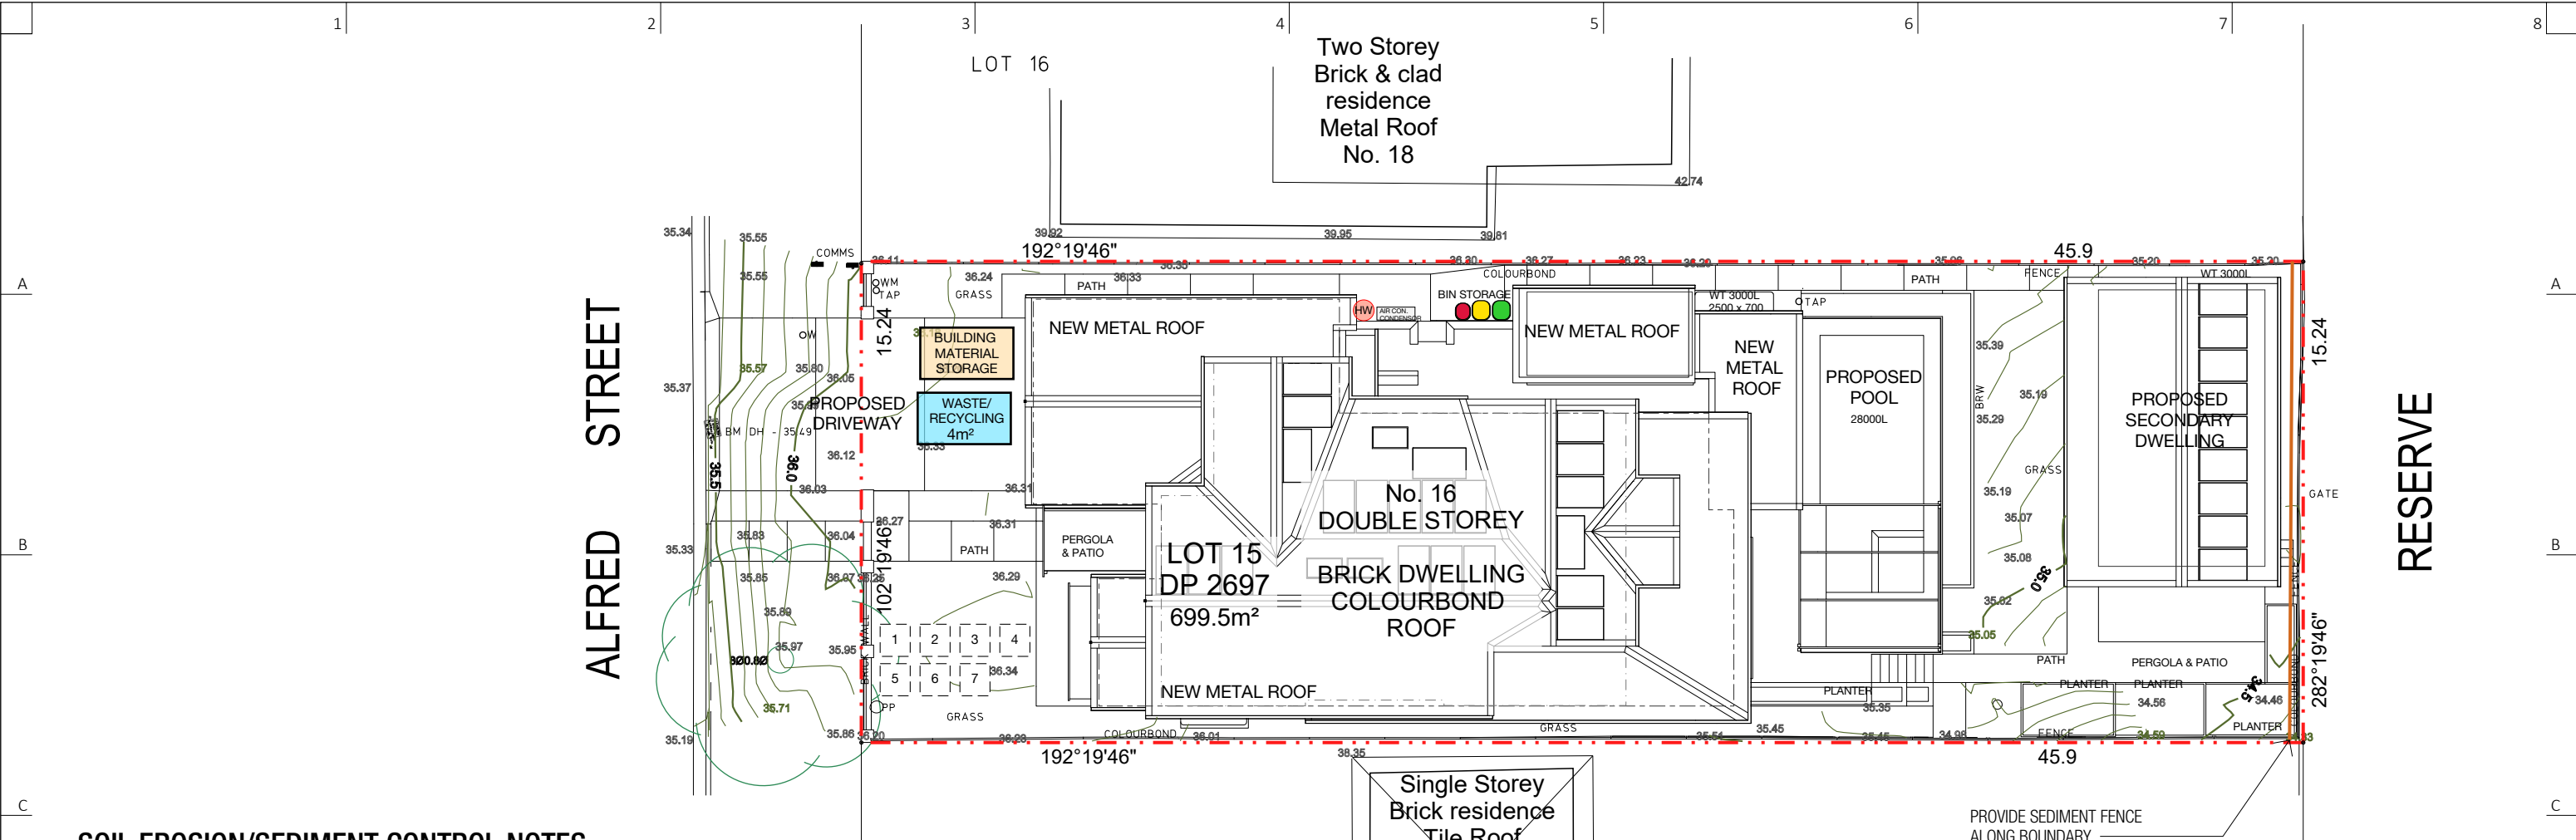

SOIL EROSION/SEDIMENT CONTROL NOTES

- SEDIMENT FABRIC SUCH AS TERRAAM 100, POLFELT TS 500, BIDIM U24, GEOFAB, ENVIROFENCE OR EQUIVALENT TO BE PROVIDED ON ALL BOUNDARIES AS REQUIRED.
- FABRIC IS ATTACHED TO A STRAND WIRE (ORDINARY FENCE WIRE) OR WIRE MESH (14 GAUGE AND 150MM X 150MM OPENING).
- THE LOWER END OF THE FABRIC AND MESH TO BE EMBEDDED 200MM INTO THE GROUND.
- FILTER CLOTH TO BE FASTENED SECURELY TO WIRE FENCE WITH TIES SPACED EVERY 600MM.
- GENERALLY FOLLOW THE CONTOUR OF THE LAND.
- WHEN 2 SECTIONS OF FILTER CLOTH ADJOIN EACH OTHER THEY SHALL BE OVERLAPPED BY 150MM AND FOLDED OVER.
- POSTS HOLDING THE MESH ARE EITHER STEEL Y OR U TYPE OR 45-50MM HARDWOOD 900-1200MM LONG POSTS. THESE ARE TO BE SPACED 2-3M APART.
- STOCK PILES ARE TO BE SET UP WITH SEDIMENT CONTROL DEVICES ON THE LOWER SLOPE.
- TEMPORARY BARRIERS CONSTRUCTED FROM TIMBER, SYNTHETIC FABRICS, JUTE, STRAW BALES, BRUSH OR SIMILAR MATERIALS CAN BE USED TO CONTROL AIR CURRENTS AND BLOWING SOIL. THEY SHOULD BE PLACED AT RIGHT ANGLES TO THE PREVAILING WIND AND SPACED AT INTERVALS EQUIVALENT TO ABOUT 15 TIMES THEIR HEIGHT.

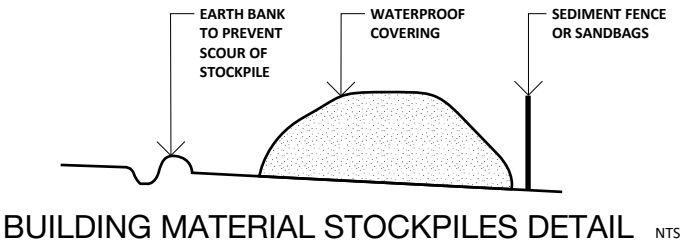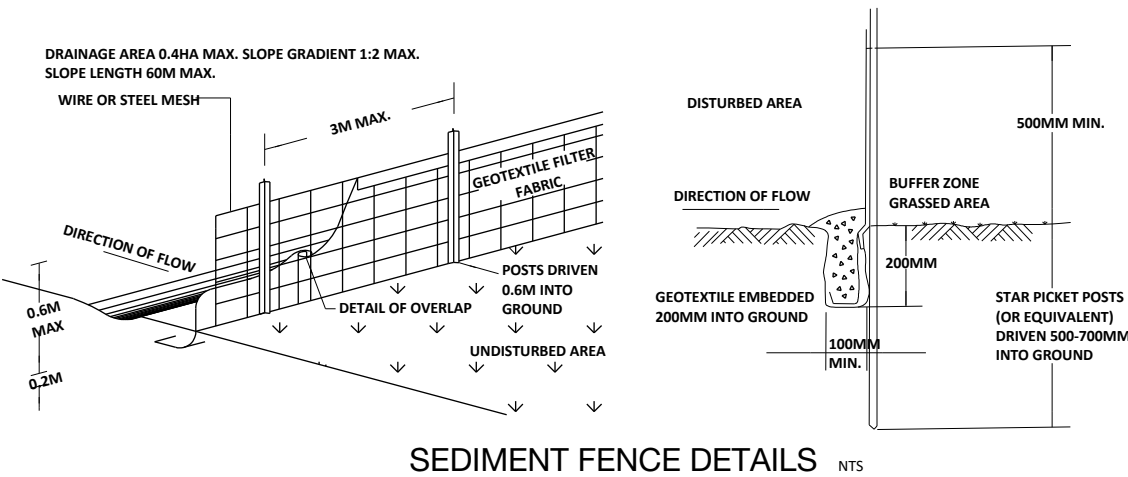

WASTE BAYS	
STOCKPILE No.	MATERIAL TYPE
1	CONCRETE
2	LANDFILL
3	PLASTERBOARD
4	PAPER PACKAGING
5	METALS
6	TIMBER
7	INSULATION / PLASTICS

WASTE MANAGEMENT NOTES

- VEHICLES TO BE HOSED DOWN TO PREVENT SOIL/EXCAVATED MATERIAL BEING DEPOSITED ON ROADWAY.
- CONCRETE PUMPING, DELIVERY OF MATERIAL, LOADING AND UNLOADING OF MATERIAL TO BE DONE WITHIN THE CONFINES OF THE PROPERTY
- WASTE BAYS 1-4 ARE TO BE CONSTRUCTED USING SHADE CLOTH OR SEDIMENT FENCING. WHERE THE WASTE STREAM IS MADE UP OF LIGHT MATERIAL SUCH AS PAPER AND CARDBOARD, THE WASTE BAYS MUST CONSIST OF A CONTAINER FOR THE STORAGE OF THIS MATERIAL.
- A METAL WASTE CONTAINER (5) WITH A MINIMUM CAPACITY OF FOUR CUBIC METRES MUST BE PROVIDED ON SITE FOR THE DISPOSAL OF "GENERAL WASTE" DESIGNATED FOR LANDFILL

01 Site Waste Management Plan
SCALE: 1:200

DEVELOPMENT APPLICATION MODIFICATION
DO NOT USE THIS DRAWING FOR CONSTRUCTION UNLESS DESIGNATED